PORTFOLIO

Jacopo Dellanoce



Jacopo Dellanoce

Sono uno studente del Politecnico di Milano della facoltà interior design. Il mio percorso affonda le radici nel liceo scientifico, dove ho iniziato a coltivare la passione per il disegno e per la progettazione, intesa come processo in grado di tradurre un’idea in un’opera concreta. Questa curiosità mi ha condotto verso il mondo dell’interior design, che ho approfondito durante il triennio, nel corso del quale ho maturato un interesse specifico per l’exhibit design, ambito che desidero continuare ad approfondire, insieme ai progetti di riqualificazione di aree e spazi urbani in disuso, temi che considero centrali per una progettazione consapevole e sostenibile.Il lavoro in team ha rappresentato un elemento significativo della mia formazione: la partecipazione a progetti collettivi mi ha permesso di affinare capacità di confronto, ascolto e sintesi tra visioni diverse, arricchendo il mio approccio metodologico.

Exhibit

01



OltrEtrusco


02



Unseen

Interior

03

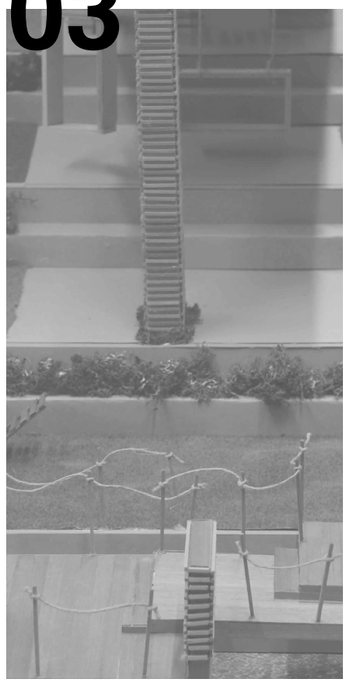

Lighthouse

04



Uno + Uno

05



Workshop

01
OltrEtrusco

Corso
Politecnico di Milano, secondo anno, Laboratorio di design degli interni
Docenti
R.Trocchianesi, A.Mazzanti
Progettisti
Noè Bartolini**, Jacopo Dellanoce,** Luca Mastromatteo, Anton Qerkini, Filippo Antonio Visentin

Sito di progetto

La mostra, situata nel complesso museale di Santa Chiara a San Gimignano in Toscana, costruisce un percorso in sei sale in cui opere antiche e contemporanee dialogano direttamente, rivelando continuità formali e simboliche tra la civiltà etrusca e il mondo contemporaneo.


Concept


Sconfinare è la metafora utilizzata per la progettazione dell'allestimento. L'obiettivo è quello di far comprendere come la civiltà Etrusca sia sconfinata nell'era moderna grazie agli innumerevoli spunti di riflessione da essa derivanti. Sono presenti artefatti antichi e moderni, messi in confronto in modo che sembrino gradualmente della stessa epoca. L'atteggiamento progettuale è stato intrapreso al fine di far coincidere la metafora spaziale e il tema di progetto. Nell'allestimento il confine è visto come un Oltre, che perde il valore di divisione nel tempo e nello spazio.

Tema


La mostra nasce dal desiderio di unire linguaggi e tempi diversi attraverso la metafora del confine. L'allestimento costruisce un percorso in cui opere antiche e contemporanee dialogano direttamente, rivelando continuità formali e simboliche. Ogni sala diventa una soglia da attraversare, dove le forme si rispecchiano e le identità culturali si sovrappongono. La curatela invita a riconoscere che il passato non è distante, ma una presenza che nutre costantemente il nostro sguardo.




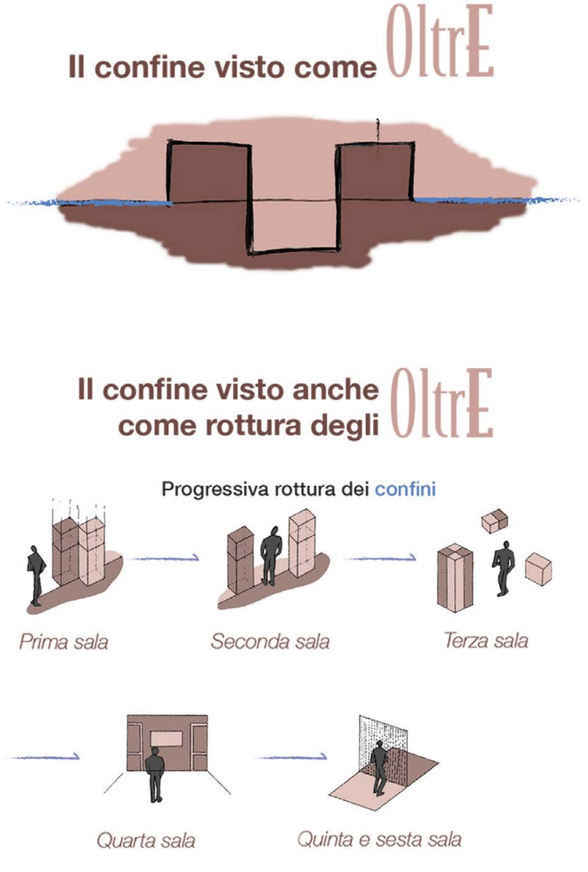


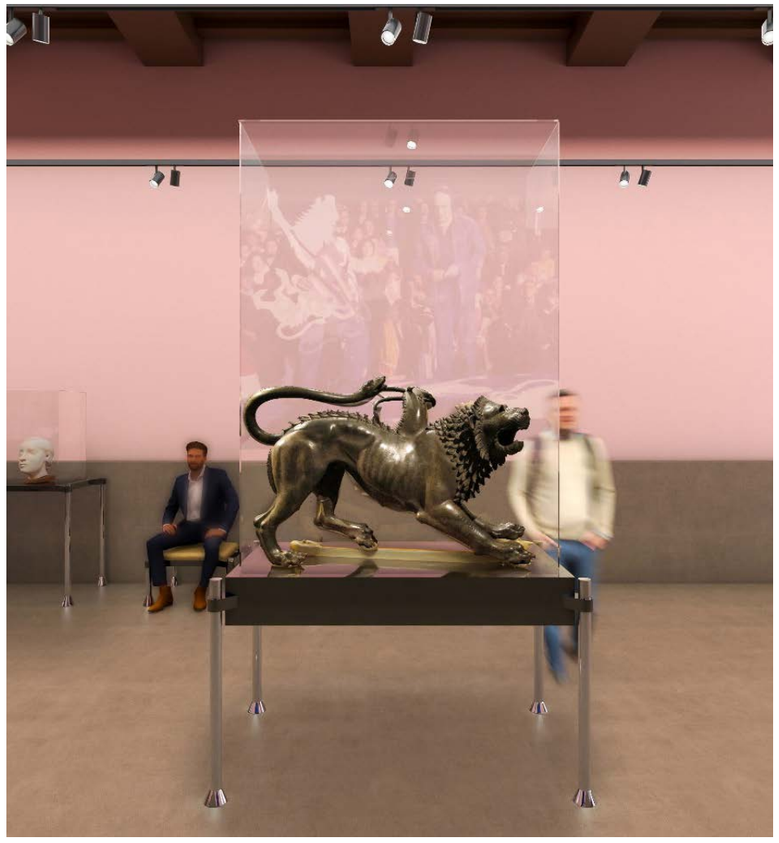


Sezioni

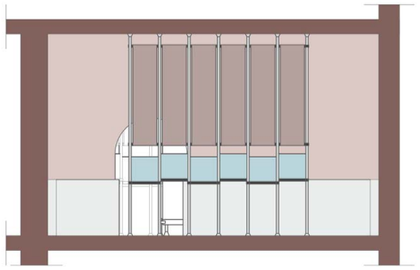


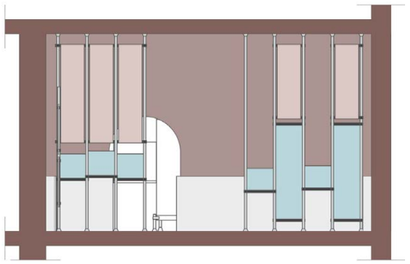

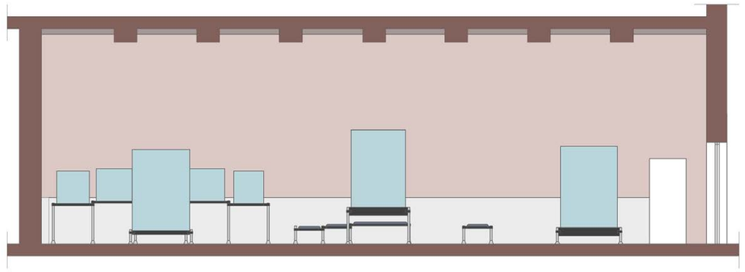


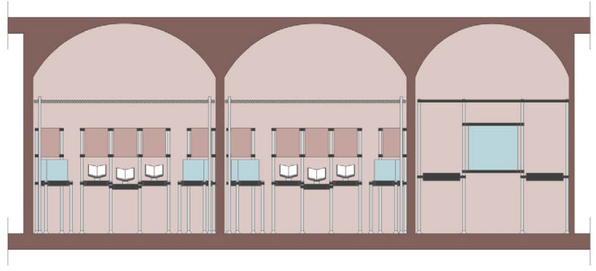

Pianta

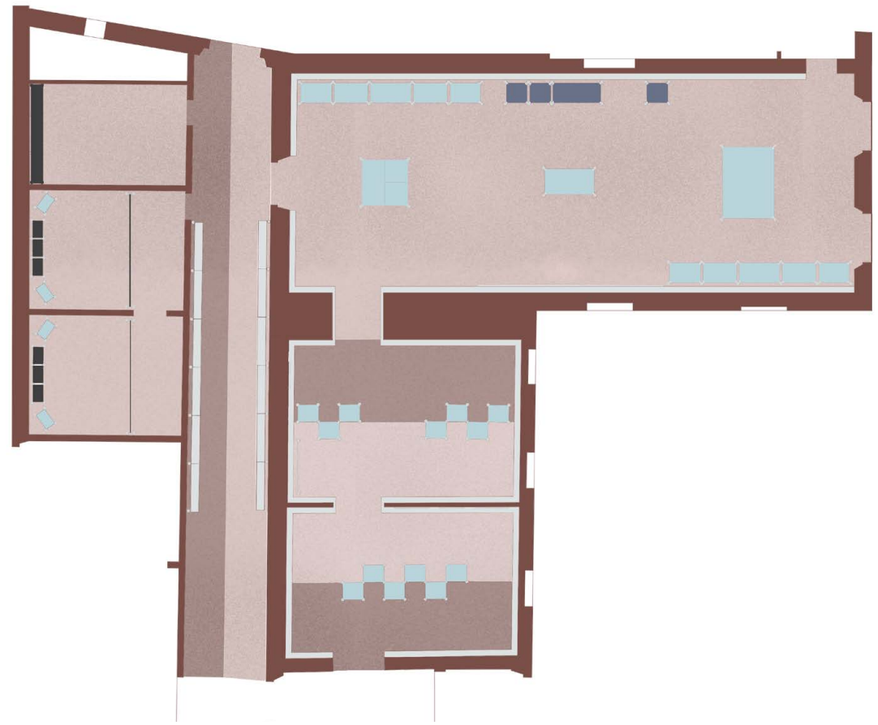


Esploso

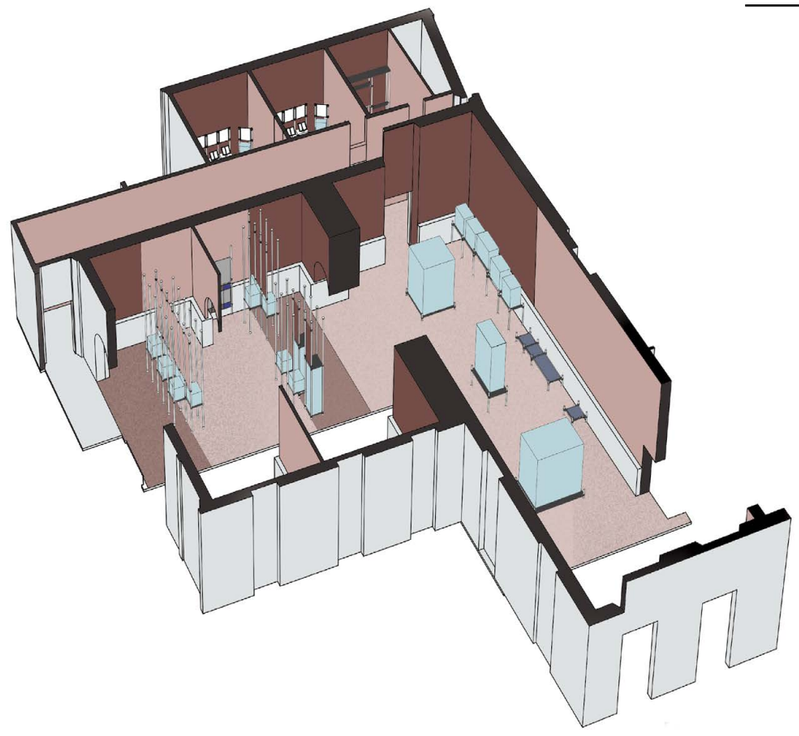


Prima sala

Quotidianità I: il vasellame

La sala esplora la quotidianità attraverso il vasellame, affiancando reperti etruschi alle opere di Picasso, Gio Ponti e Mario Schifano. Le corrispondenze formali e concettuali mostrano come l'eredità mediterranea attraversi la storia del design e dell'arte moderna.

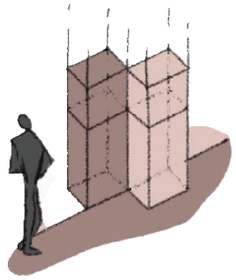


Confine netto e definito, percorso obbligato

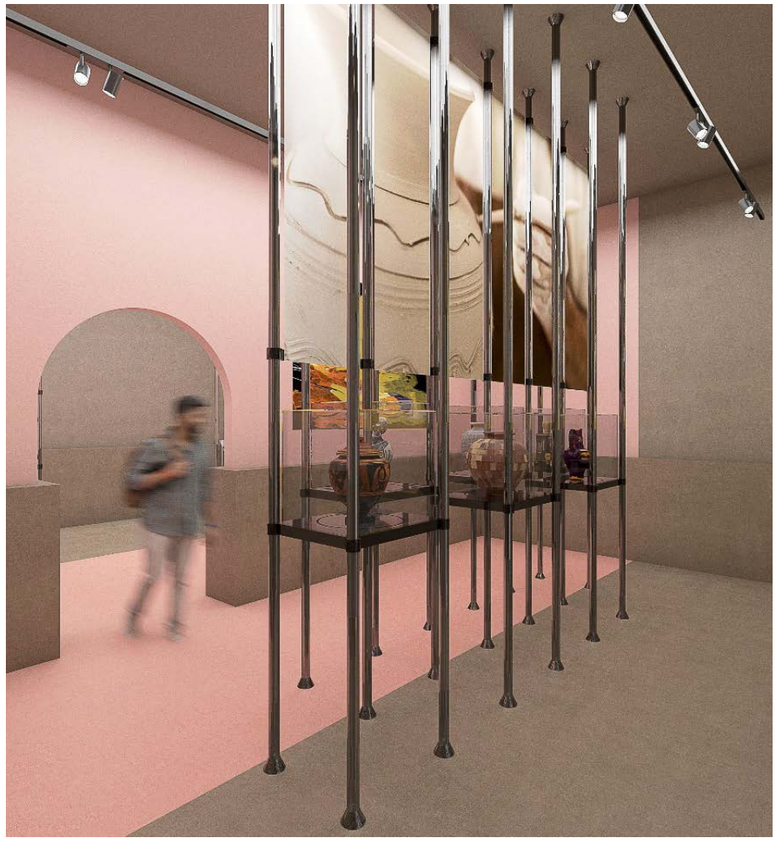


Seconda sala

Quotidianità II: la moda e la cura del corpo

La sala affronta moda, cura del corpo e profumi, temi centrali nella cultura etrusca e ancora attuali. Ai contenitori per unguenti e agli oggetti rituali si affiancano le illustrazioni di Maddalena Sisto e capi contemporanei ispirati ai drappeggi antichi, a conferma della continuità estetica tra passato e presente.

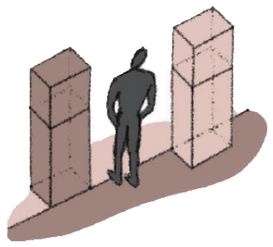


Confine rotto a metà, percorso semi-libero

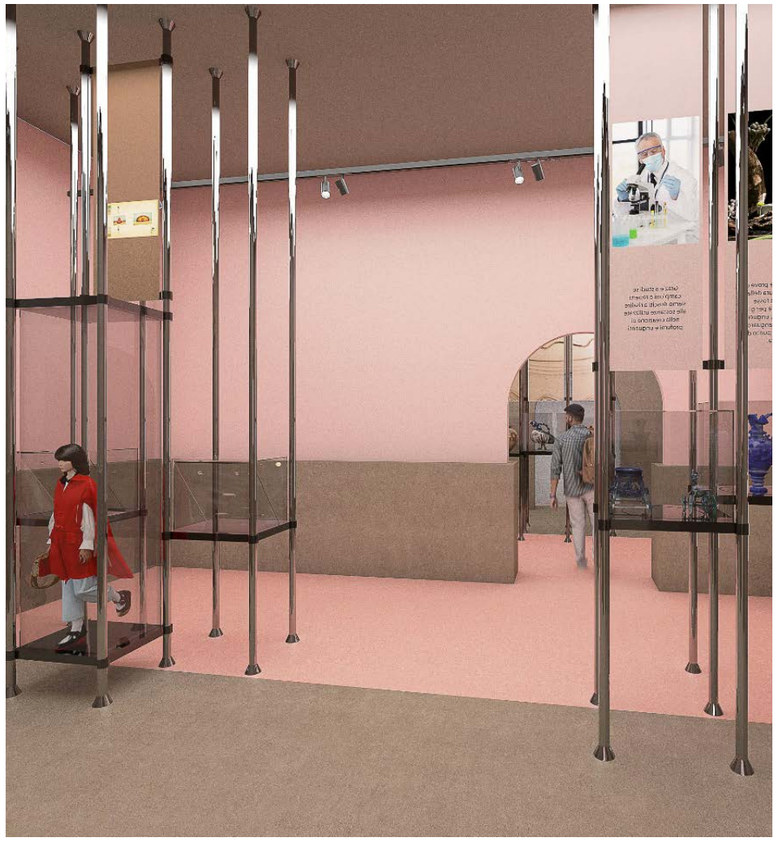


Terza sala

Arte e Guerra: opere d'arte e artefatti bellici

La sala è dedicata al rapporto tra arte e guerra: statue votive, armi e bronzi etruschi dialogano con le opere di Marino Marini, Giacometti e Giacomo Verde. Ne risulta un ambiente sospeso nel tempo, dove le figure antiche sembrano moderne e quelle moderne sembrano provenire da un'archeologia futura.

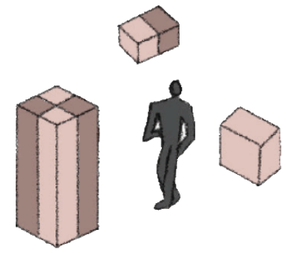


Confini distribuiti in tutto lo spazio, percorso libero

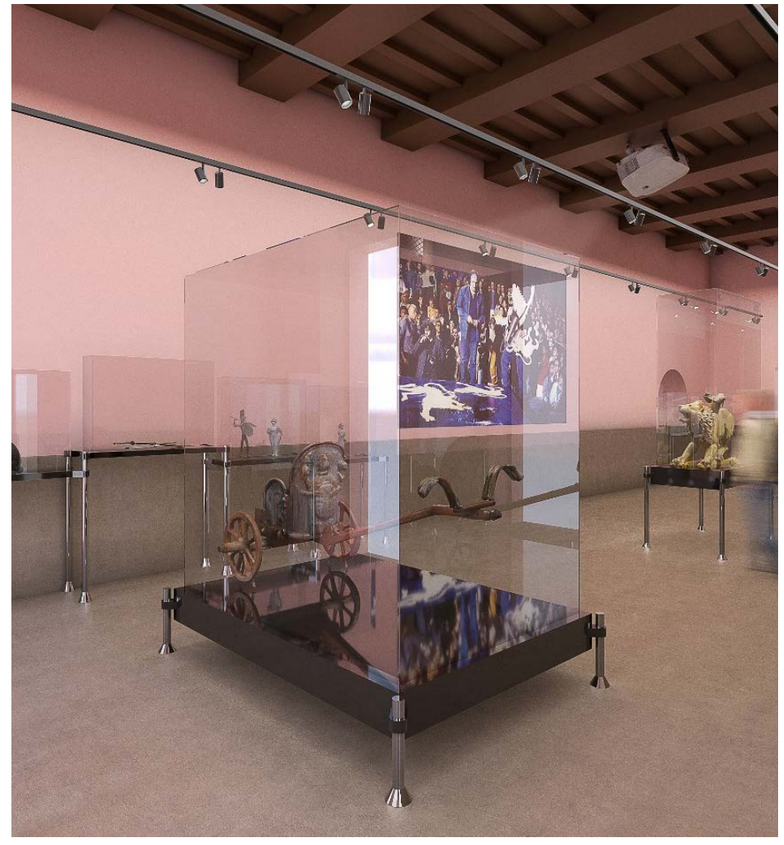


Quarta sala

La morte

La sala ricostruisce la Tomba degli Auguri, riletta da Schifano. Antico e contemporaneo si fondono in un'unica immagine, invitando a riflettere sul ruolo del rito e sul linguaggio della memoria**.**

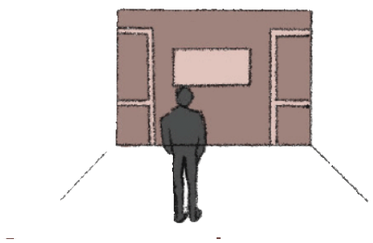


Confine oltrepassato dal soggetto del quadro che torna ambiente

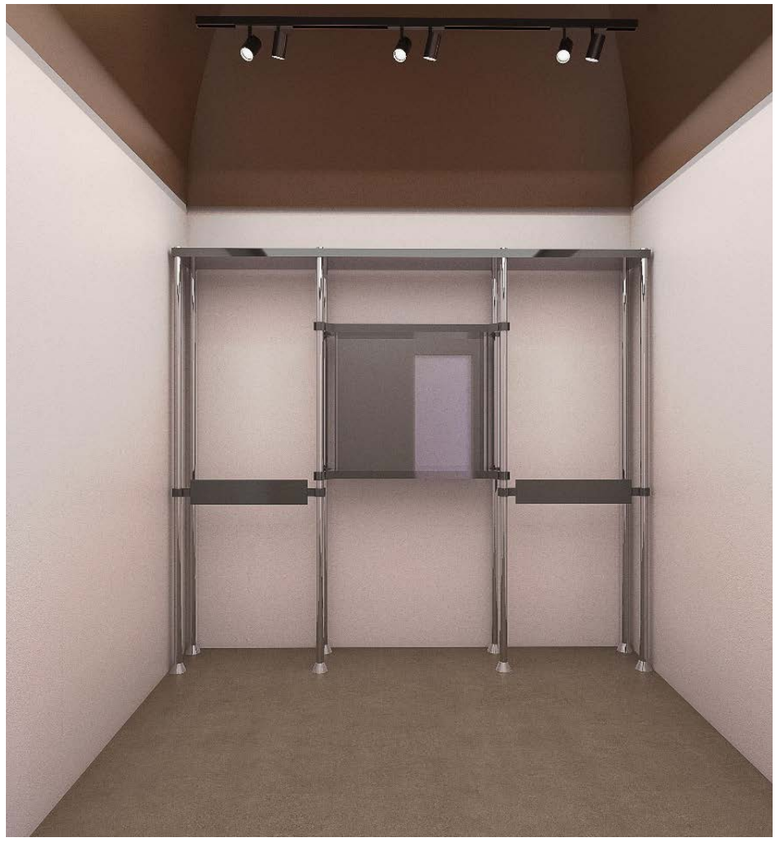


Quinta e sesta sala

Etruschi nella modernità

Le ultime sale propongono i cataloghi delle mostre moderne fondamentali sugli Etruschi, esposti in ordine cronologico.

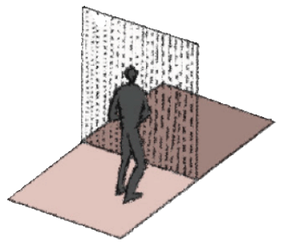



Confine rotto a metà, percorso semi-libero

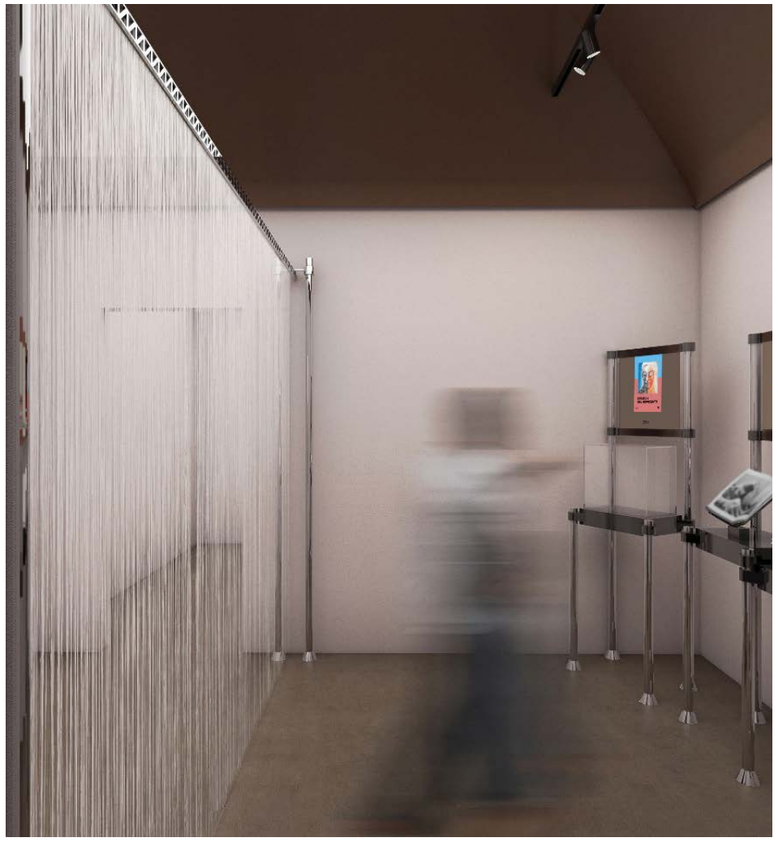

Corridoio


Passaggio tra antico e moderno

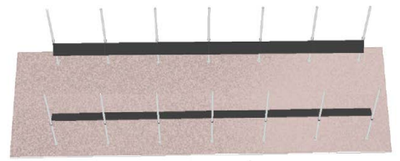

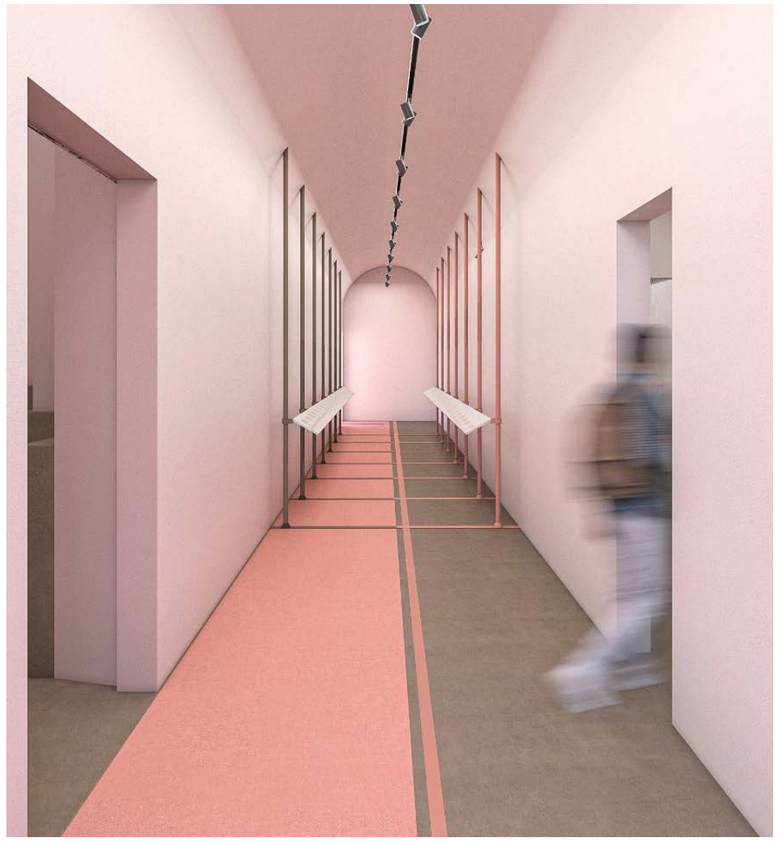


Partitura allestitiva


La partitura allestitiva è uno strumento di lettura sintetica del progetto, capace di restituire in un unico apparato grafico le logiche compositive che regolano l'intera mostra, sala per sala. Il sistema sovrappone cinque livelli di analisi: organizzazione dei contenuti, distribuzione spaziale, artefatti espositivi, interazione tra visitatore e allestimento, tempo di percorrenza, leggibili sia singolarmente sia in relazione reciproca, per verificare la coerenza tra impianto narrativo e soluzioni allestitive.La partitura rende quindi esplicito il criterio con cui ogni sala calibra densità dei contenuti, tempo di permanenza e grado di coinvolgimento del visitatore, trasformando la sequenza espositiva in una struttura misurabile e confrontabile.

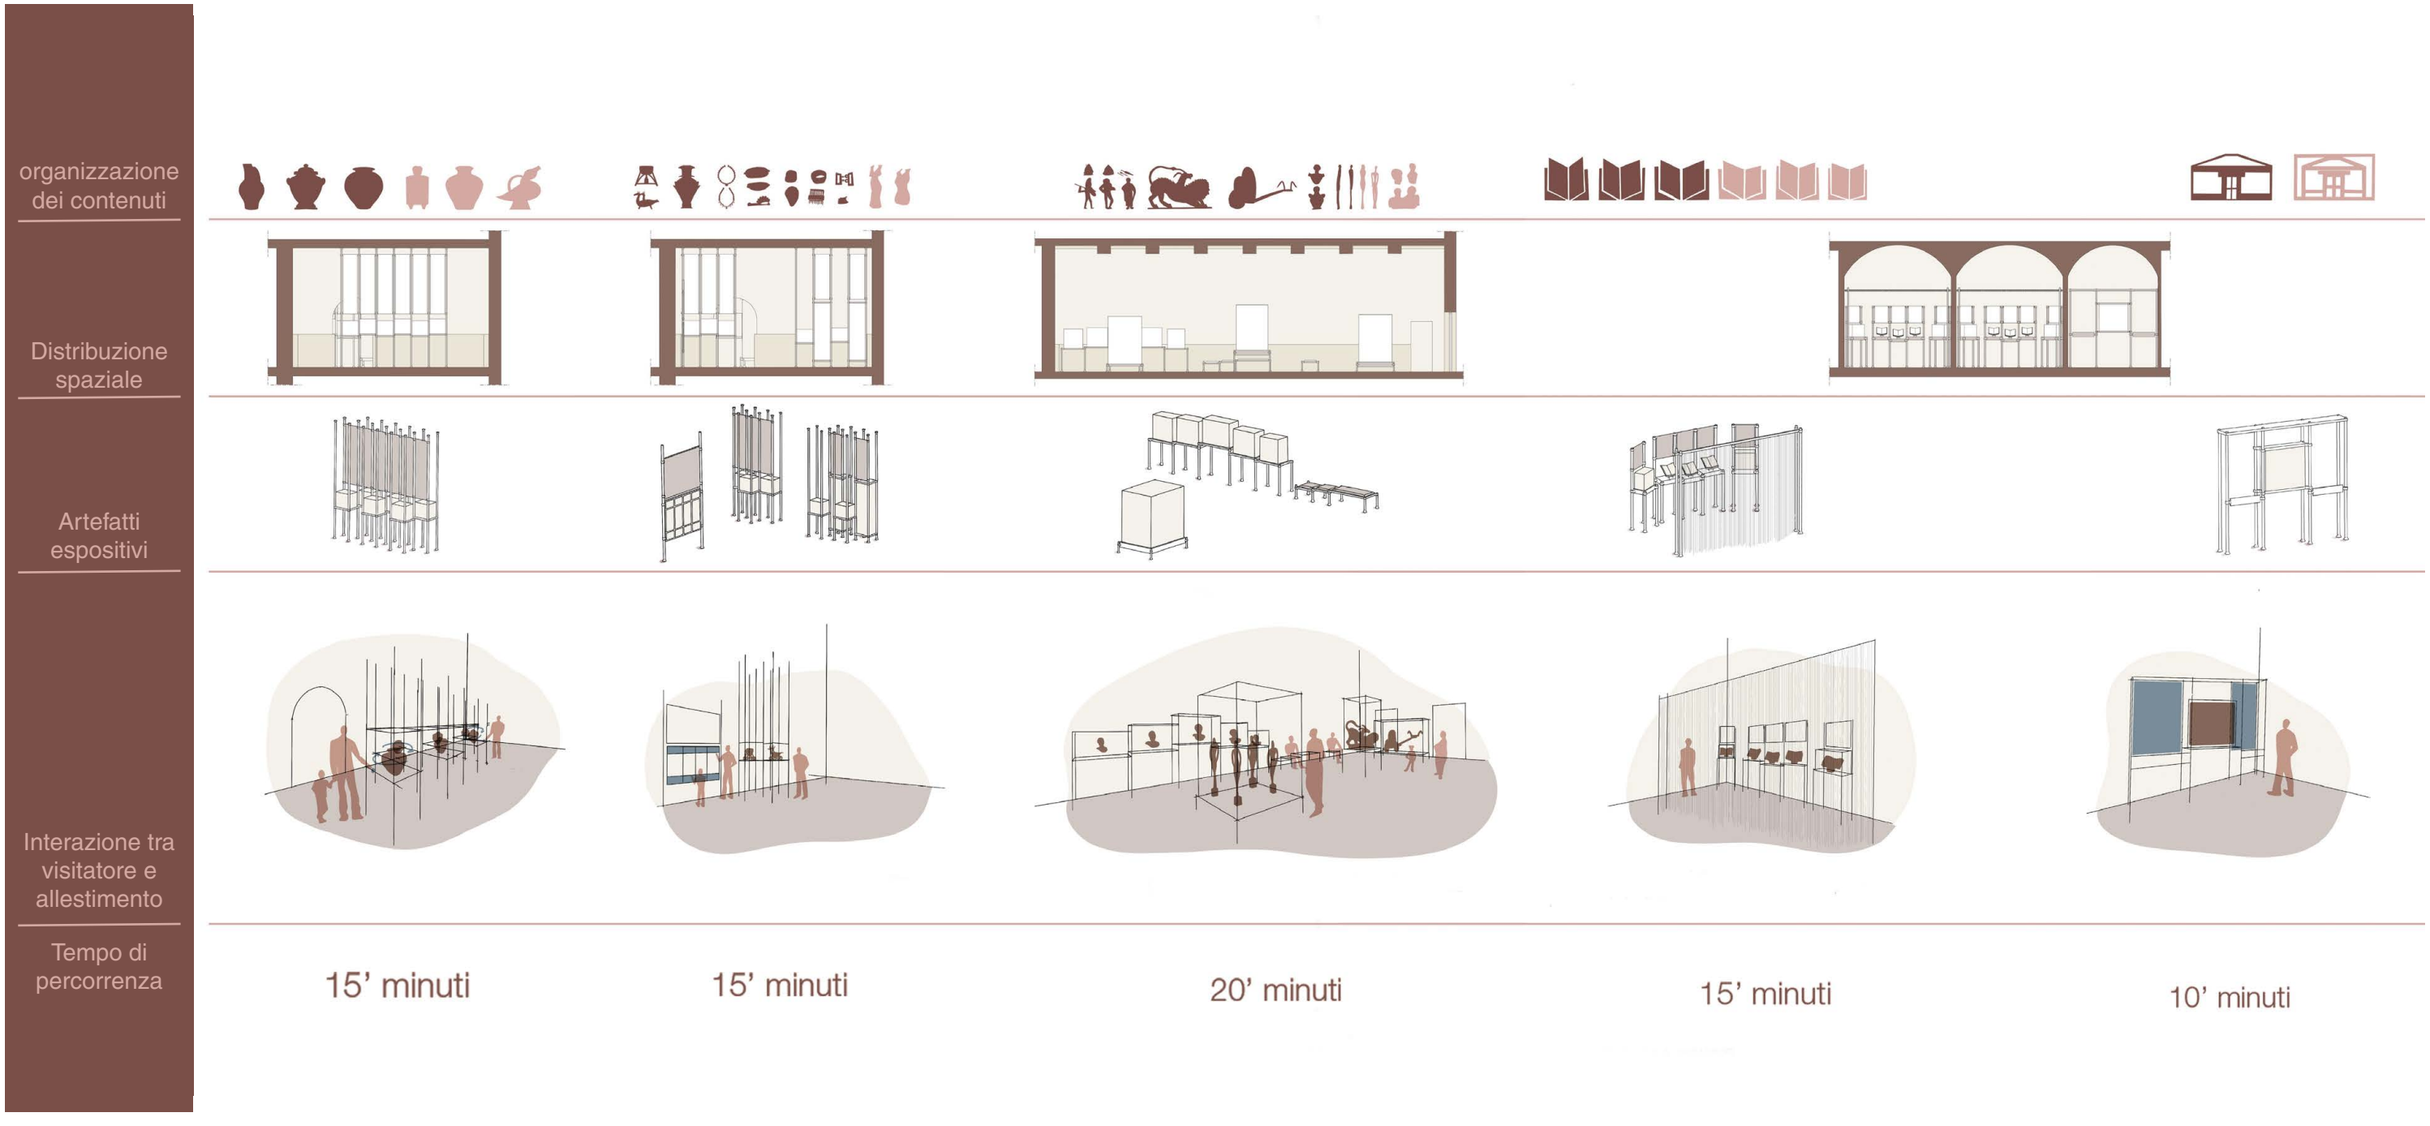

Catalogo opere



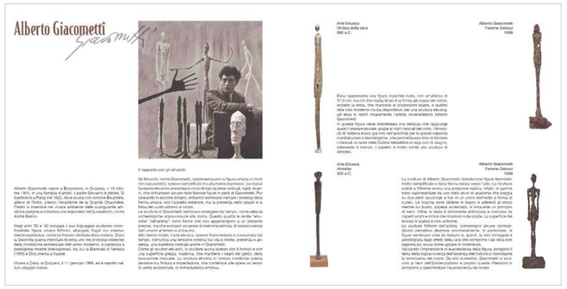

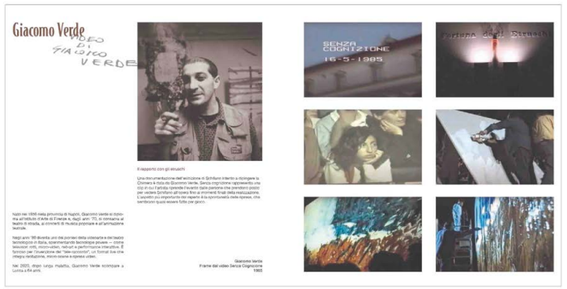

Mostra

Il progetto è stato esposto alla mostra “Anima etrusca” tenuta nel complesso museale di Santa Chiara a San Gimignano.







Manifesto



La Toscana, antica culla della civiltà etrusca, conserva nei suoi paesaggi, città e tradizioni i segni di un’eredità viva.
Qui il passato etrusco dialoga ancora con il presente, intrecciando cultura, forma e identità in un continuum senza tempo.

3-19 Settembre, 2025
Palazzo Comunale,
Pinacoteca
San Gimignano, SI

OltrEtrusco



02
Unseen

Corso
Pilitecnico di Milano, terzo anno, Laboratorio di sintesi finale
Docenti
Raffaella Trocchianesi, Ilaria Bollati, Ares Bolognesi,Paolo Maria Fumagalli
Progettisti
Jacopo Dellanoce, Margherita Manto, Luca Mastromatteo, Valeria Paieri, Anton Qerkini

Sito di progetto

Triennale di Milano, Palazzo dell'arte






Concept

Il pozzo

Il prefisso "UN–" è inteso non come semplice negazione, ma come spazio di sospensione, di perdita di forma e di significato: una soglia linguistica che nega senza cancellare, che sottrae senza distruggere, lasciando emergere condizioni intermedie e ambigue. Il pozzo ne è la metafora spaziale: un'apertura verso il basso, un luogo in cui si scende, dove la luce si perde ma il senso si concentra. Il percorso espositivo accompagna il visitatore in unmovimento verticale che invita a guardare l'interno delle cose invece della loro superficie, trasformando ogni "UN–" in una soglia da attraversare.

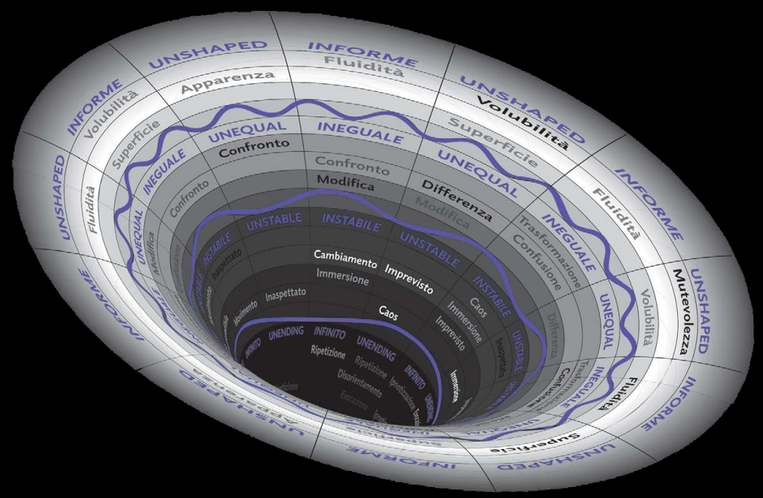

Tema


Sezioni della mostra

Unshaped:
La forma non è ancora definita. Materiali e artefatti si mostrano in divenire, prima di ogni stabilizzazione. È l'ingresso nel pozzo, dove tutto resta ancora possibile.

Unequal
Le relazioni tra gli elementi si fanno asimmetriche. Il design rivela gerarchie e tensioni: la discesa si restringe, ciò che era fluido diventa conflitto.

Unstable
Il punto di massima precarietà. Artefatti e significati sono sul punto di collassare o trasformarsi.


Unending
Il fondo del pozzo, ma non una fine: una condizione di continuità senza risoluzione. Il percorso si chiude lasciando il visitatore in sospensione.

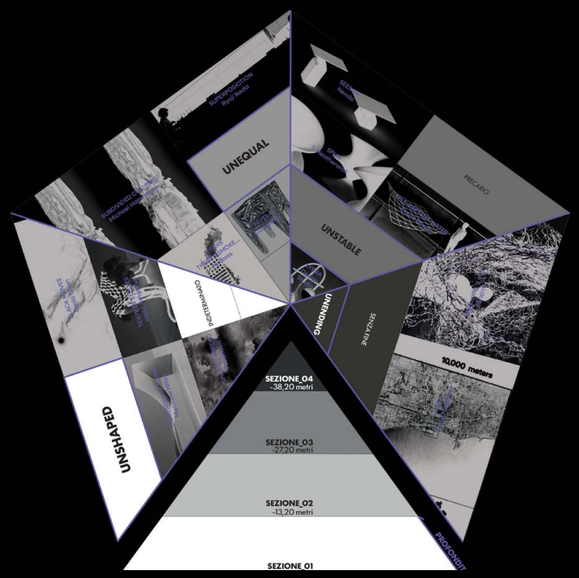

Lo spazio è diviso in quattro sezioni.


UNSHAPED | **UNEQUAL** | **UNSTABLE** | **UNENDING**

Scanzione dello spazio attraverso portali e successivo infittirsi.

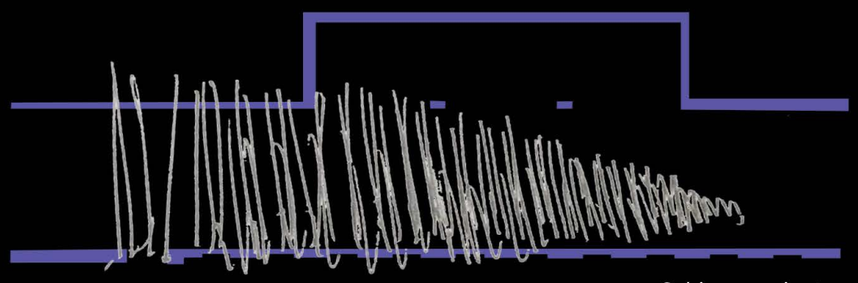


Schizzo su pianta

Progressivo abbassamento dei portali.

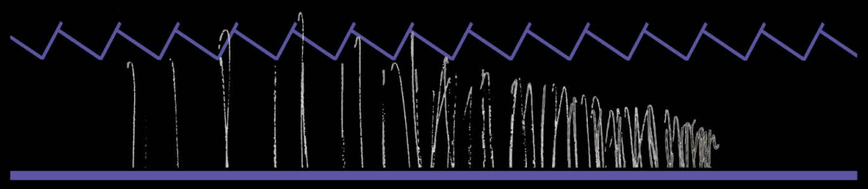


Schizzo su sezione longitudinale

Progressiva diminuzione del suono.

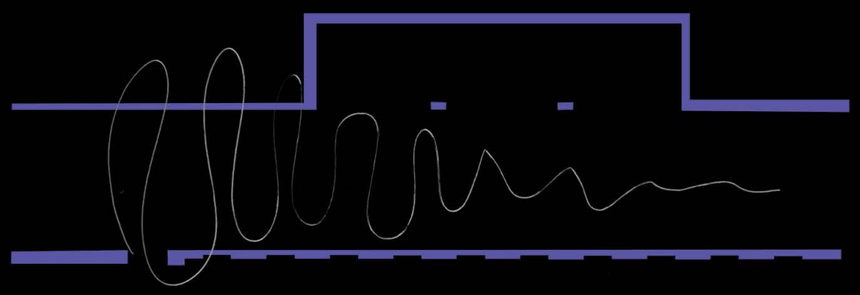

Progressiva diminuzione dell' illuminazione.

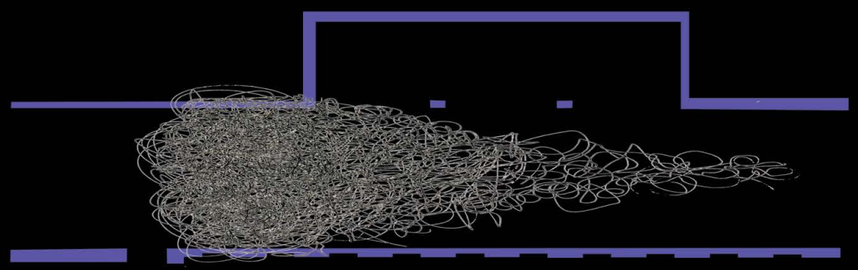


Una discesa progressiva attraverso quattro declinazioni del prefisso "UN-", tra oggetti di design e installazioni digitali.

UNSEEN è una mostra di design e media art nel Palazzo dell'Arte a Milano, in occasione del centenario Biennale 1925-Triennale 2025. Il tema dell'edizione è "Esporre e narrare mestieri e 'prodotti ad arte' tra tecnologie digitali e nuova artigianalità". L'allestimento è strutturato come una discesa simbolica in un pozzo e il percorso espositivo si articola in quattro sezioni: Unshaped, Unequal, Unstable, Unending, ciascuna corrispondente a una diversa declinazione del prefisso "UN–" (tema specifico della mostra) e a una fase della discesa.Dodici portali pentagonali, in progressiva contrazione dimensionale, scandiscono lo spazio e generano un effetto di risucchio prospettico verso il fondo. La sequenza cromatica dei pannelli, dal bianco al nero, accompagna la discesa con un parallelo sistema tecnico-percettivo: luce e suono si riducono progressivamente, traducendo in termini sensoriali l'idea di sprofondamento.




Impianto progettuale

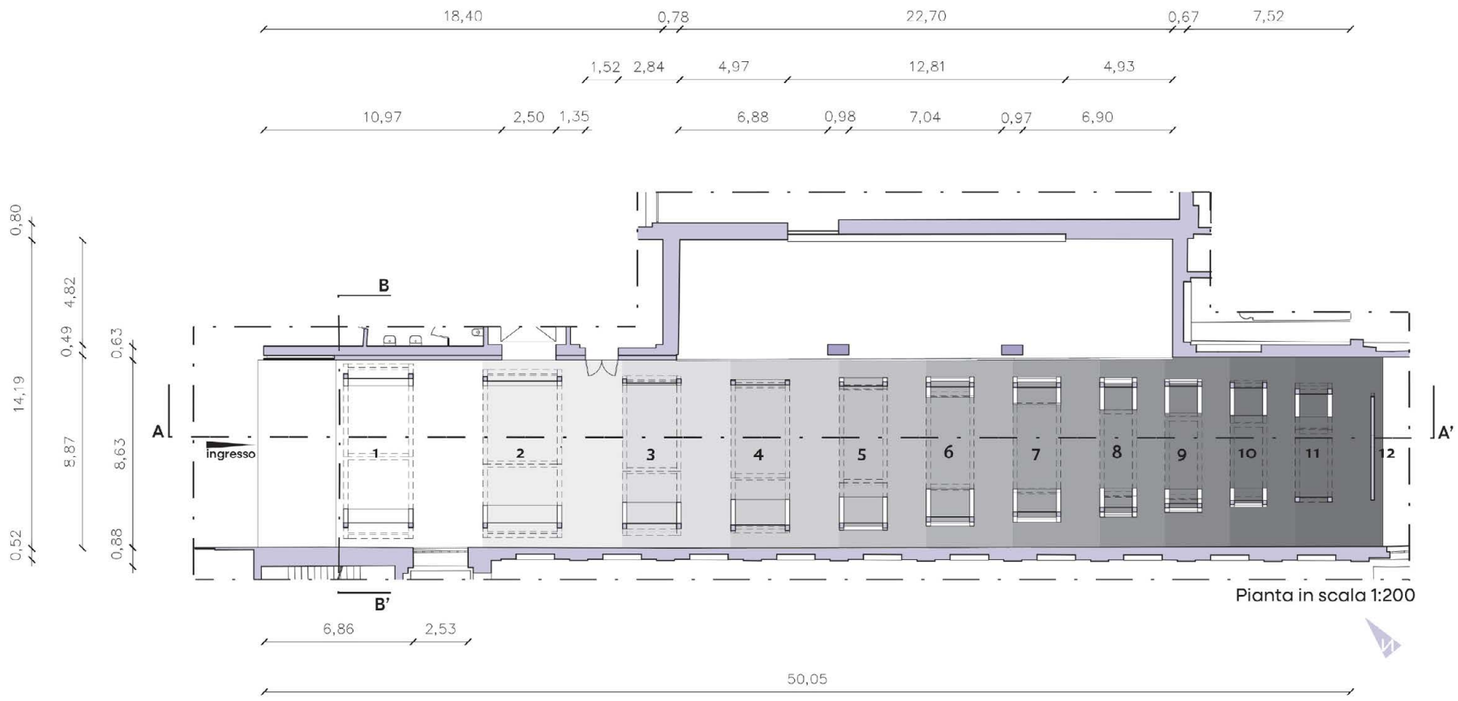



Pianta in scala 1:200

Sezione **B-B'**

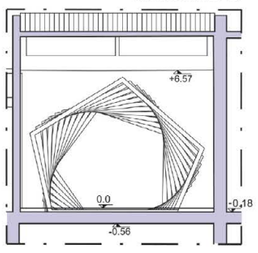


Sezione **A-A'**

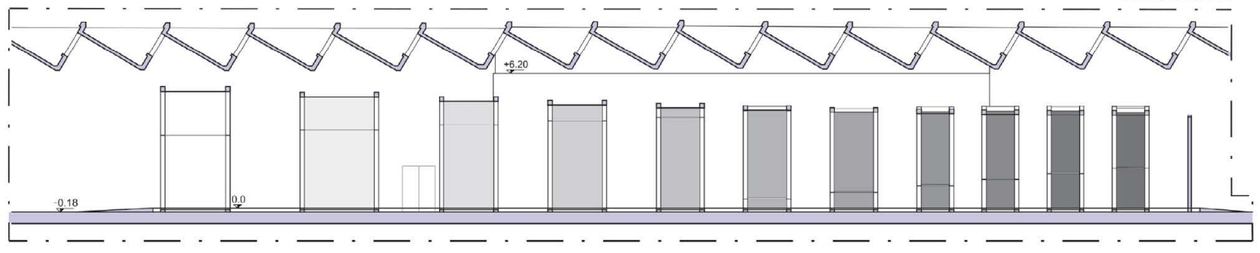


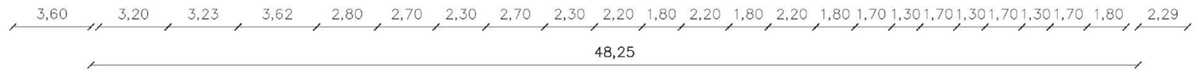

Strutture pentagonali che costituiscono i portali (due per portale)

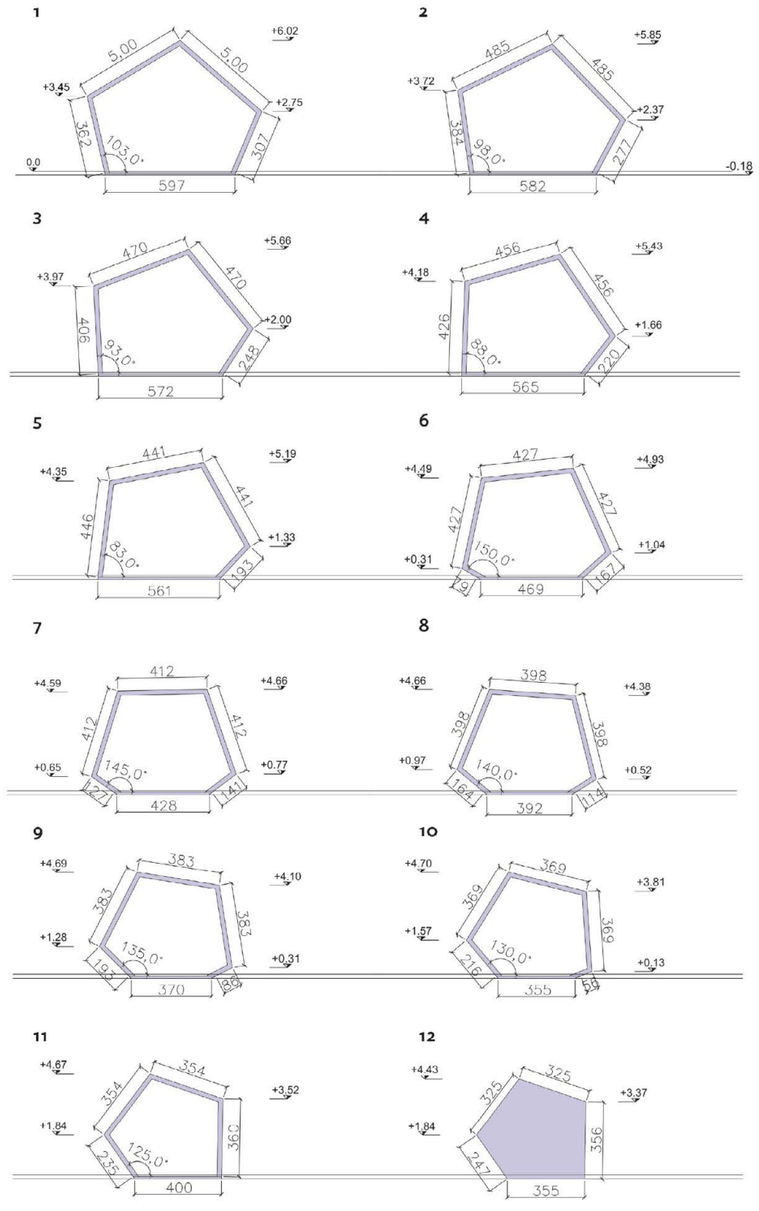


UNSHAPED

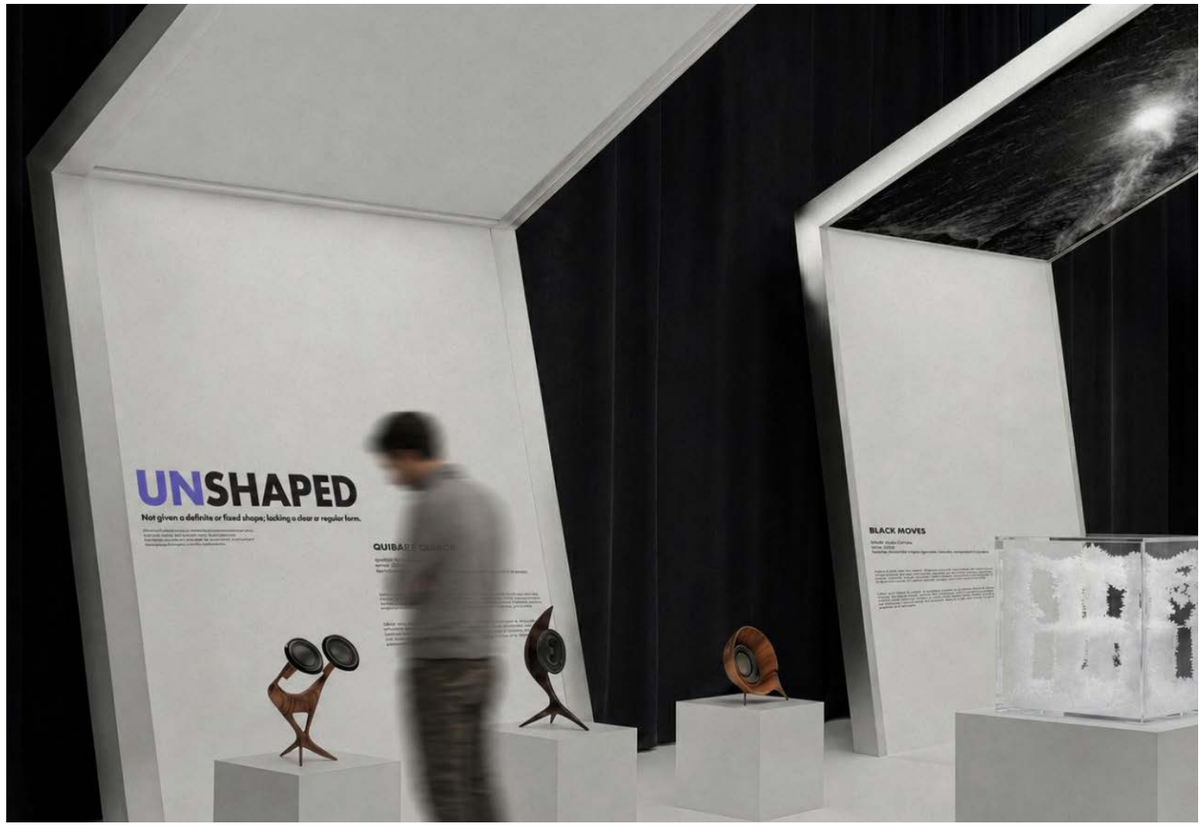
UNSHAPED
Not given a definite or fixed shape; lacking a clear or regular form.
BLACK MOVES


UNSTABLE
Without an end; continuing without interruption or final conclusion.
SPOON
FULL-PRESENT WATER


UNENDING

Partitura allestitiva

Organizzazione dei contenuti

Collocazione spaziale delle sezioni


Elementi allestitivi

Fruizione


Colore

Suono e luce

Tempo

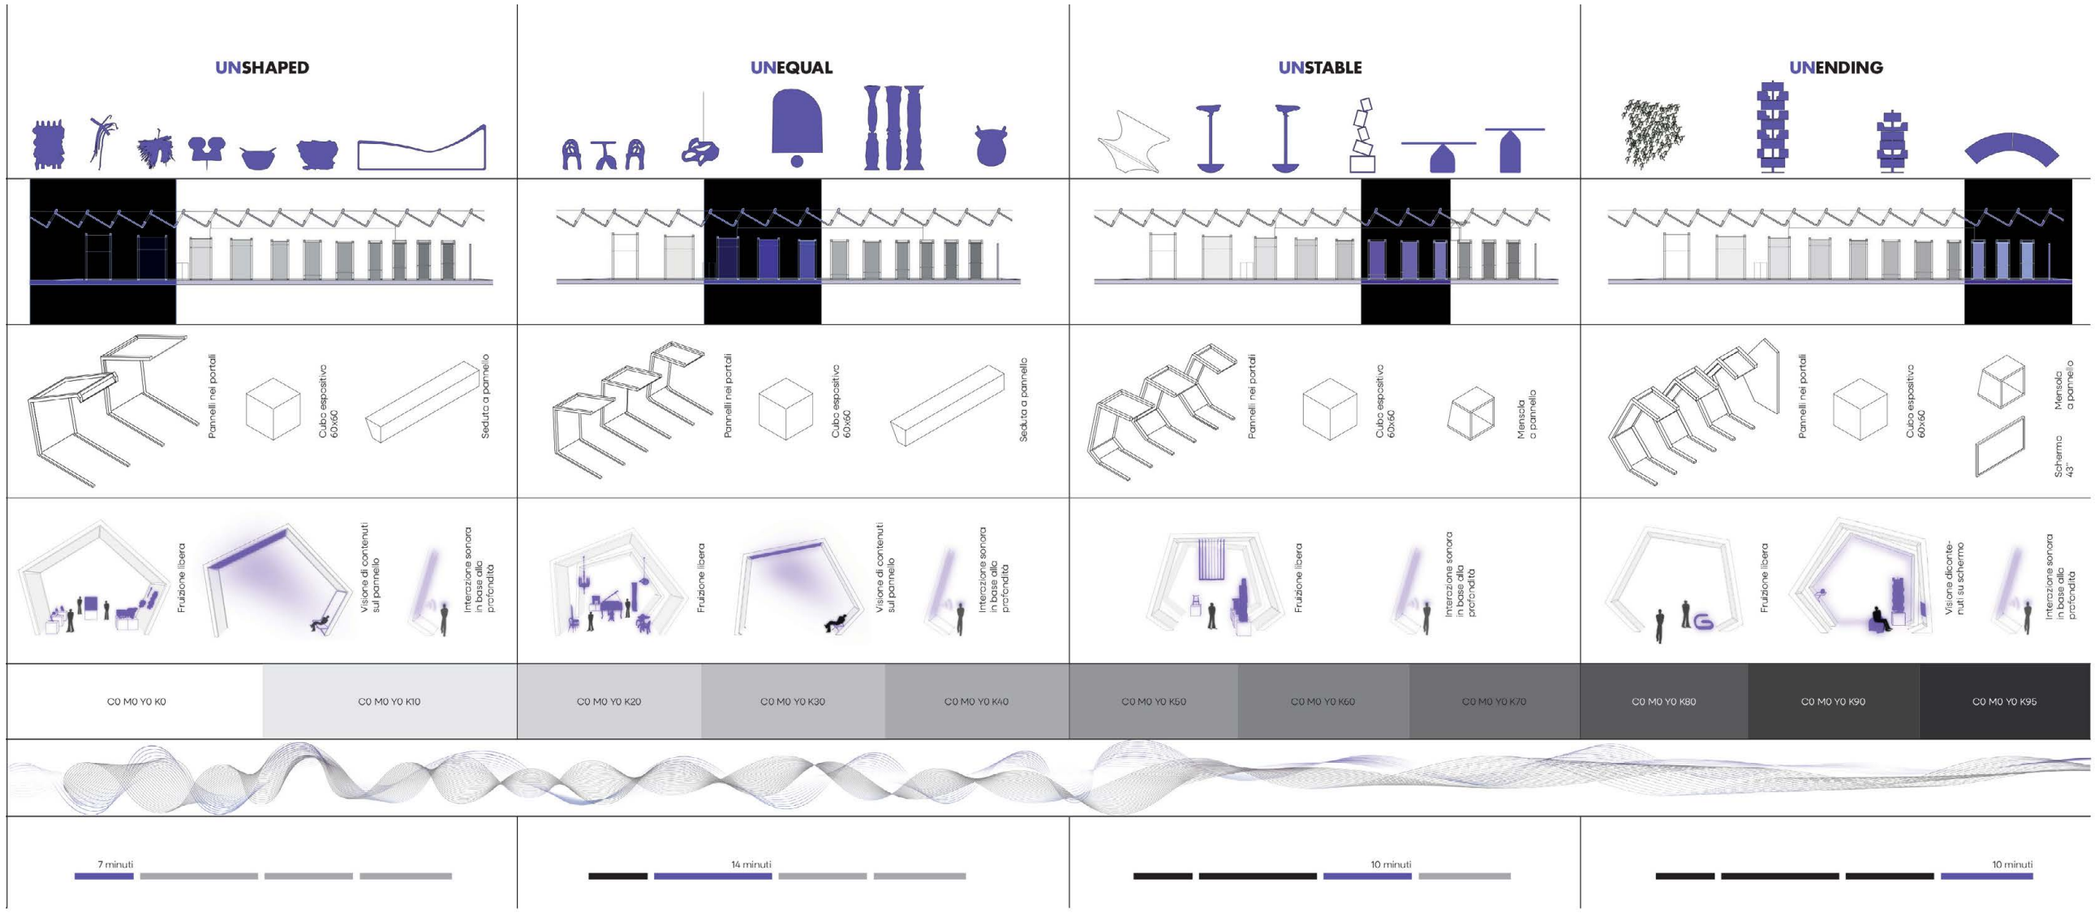



La partitura allestitiva sintetizza in un unico apparato grafico la struttura della mostra, mettendo in relazione organizzazione dei contenuti, collocazione spaziale delle sezioni, elementi allestitivi, modalità di fruizione, colore, suono e luce, e tempo di percorrenza. Lo schema legge il percorso come un climax discendente: dal bianco (UNSHAPED) al nero (UNENDING), ogni parametro, durata della sosta, intensità sonora, tipo di illuminazione, sistema espositivo (cubo, mensola), si modifica coerentemente con l'avanzare della discesa, rendendo misurabile e verificabile la corrispondenza tra concept narrativo e soluzioni progettuali.

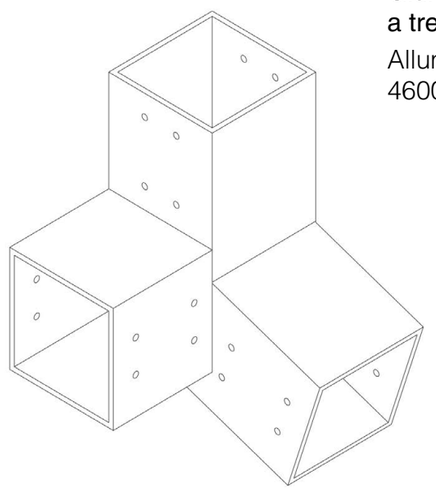


Giunto di collegamento a tre vie


Alluminio EN AC-46000

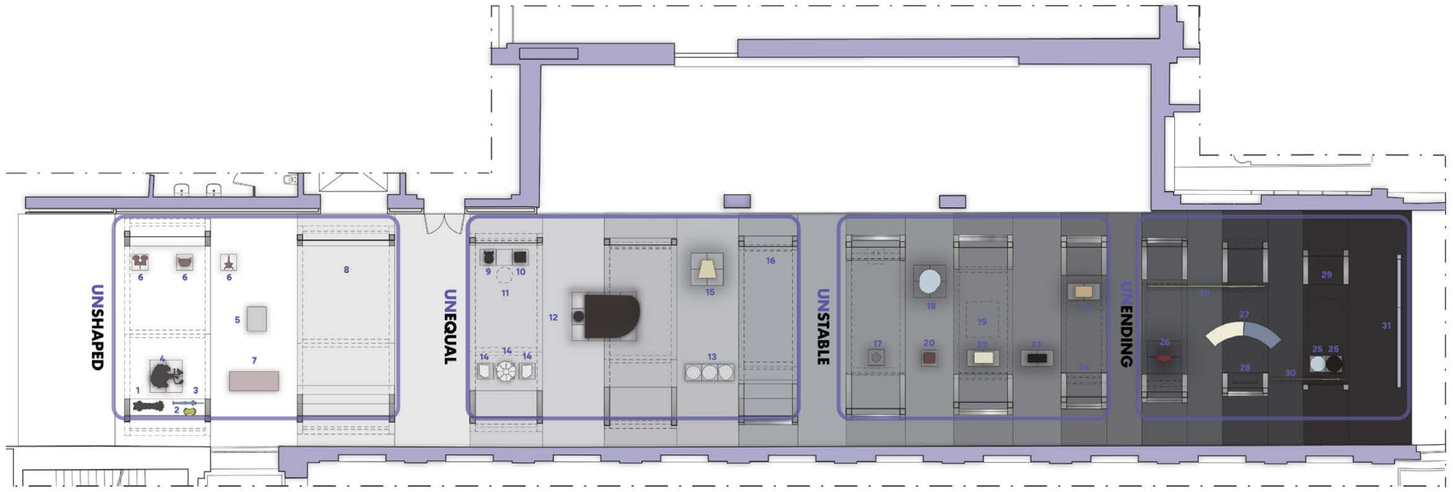

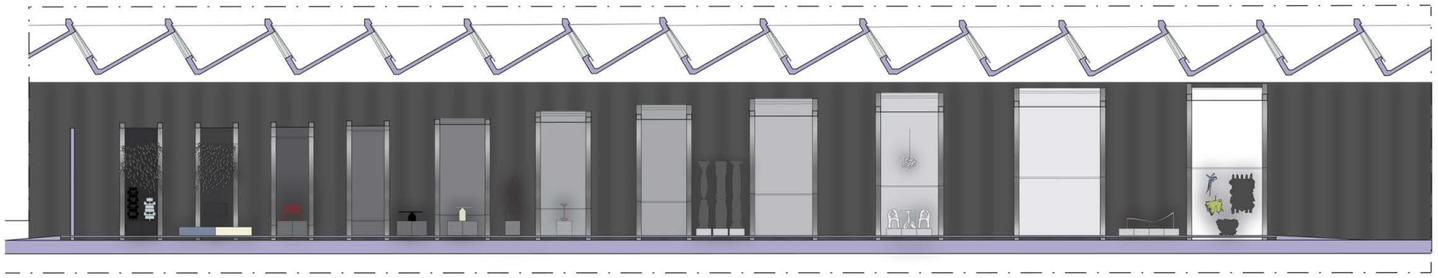


Modello

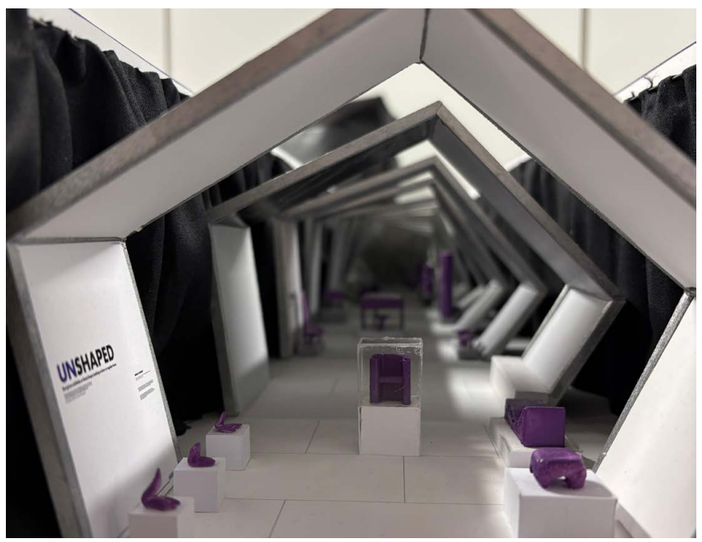

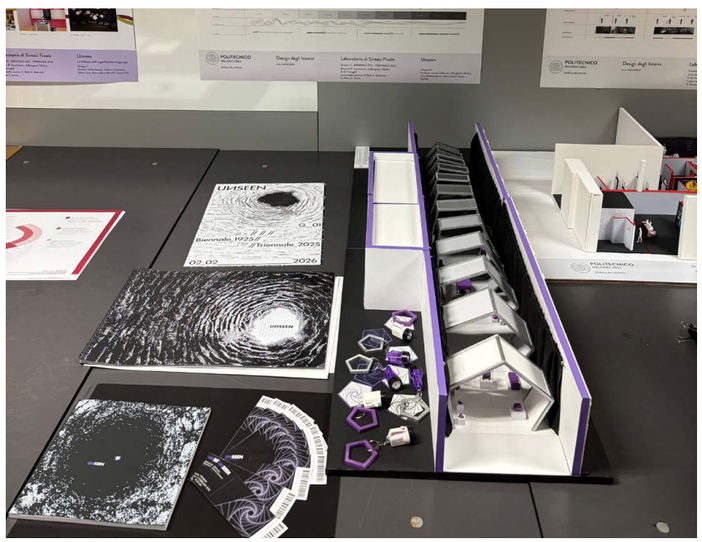

Manifesto

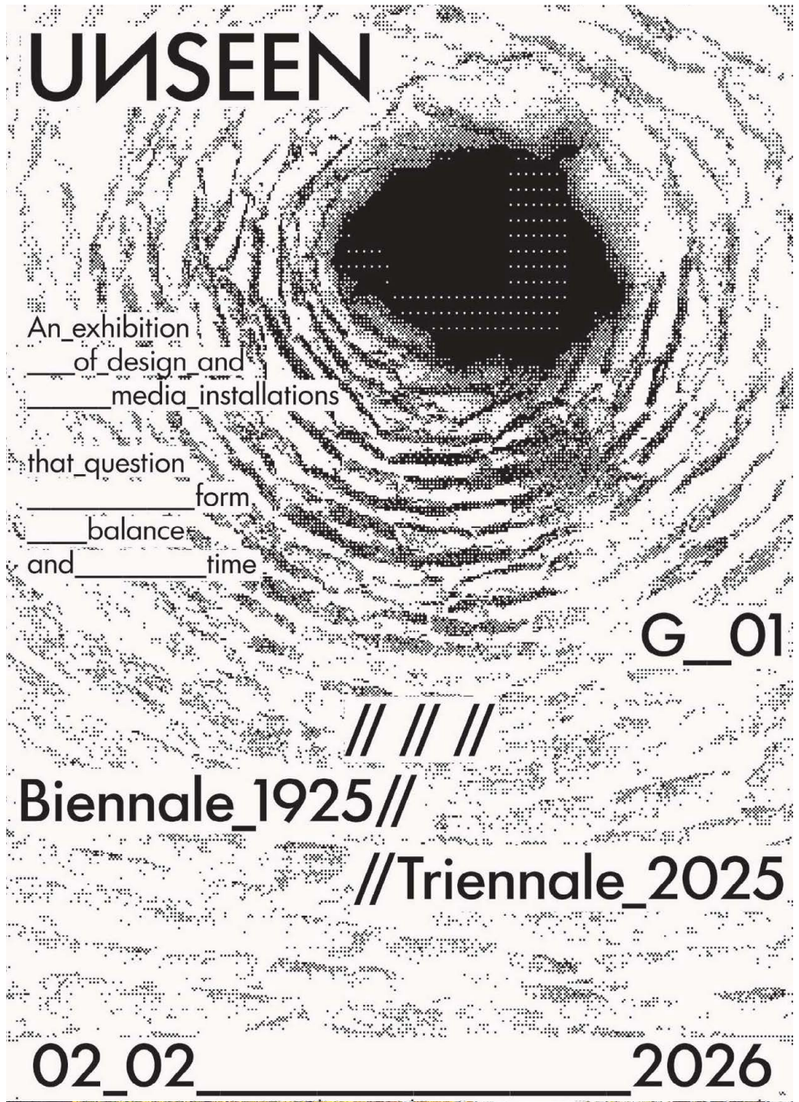



03
Light House

Corso
Politecnico di Milano, primo anno, Laboratorio di fondamenti del progetto
Docenti
Gabriella Zuco, Giulia Gerosa, Angela Mazzotti, Stefano Gigliotti, Andrea Derosa
Progettisti
Alessandra D'Avia, **Jacopo Dellanoce**, Tina Lavazza, Martina Kyoko Ruju

Sito di progetto

LAGO GHEDINA

Il progetto si colloca presso il Lago Ghedina, nelle vicinanze di Cortina d'Ampezzo, in un contesto alpino caratterizzato dalla presenza di boschi e dal rapporto diretto con lo specchio d'acqua. Il sito, ai piedi delle Tofane, presenta un ambiente raccolto e definito, in cui gli elementi naturali costituiscono il principale riferimento per l'intervento progettuale.

Tema

FRANK LLOYD WRIGHT

Frank Lloyd Wright nacque nel 1867 a Richland Center, Wisconsin. Fin da giovane mostrò una forte passione per l'architettura, che lo portò nel 1887 a trasferirsi a Chicago, dove iniziò a lavorare come allievo di Sullivan. La collaborazione tra i due durò sei anni e si interruppe a seguito di alcune committenze residenziali private accettate segretamente da Wright. Nei suoi primi lavori, Wright adottò scelte più conservative rispetto alle innovazioni del periodo e credeva fortemente che l'architetto dovesse avere un controllo completo del design architettonico, sia sugli interni che sugli esterni. I suoi progetti sono caratterizzati dall'uso attento della luce naturale, materiali grezzi come mattoni e legno, spazi continui sfruttati in orizzontale con grandi aperture e un'ottima organicità con l'esterno.


Casi studio

LAYER HOUSE

è un progetto architettonico innovativo concepito da Snøhetta, uno studio di design e architettura norvegese rinomato per le sue opere all'avanguardia.


MARMOMACC MEETS DESIGN

La mostra ha illustrato i risultati del progetto "Mutable Spirit", una sfida alla capacità di adattamento di imprese e designer, con l'obbiettivo di celebrare il marmo come materiale versatile e trasformabile.

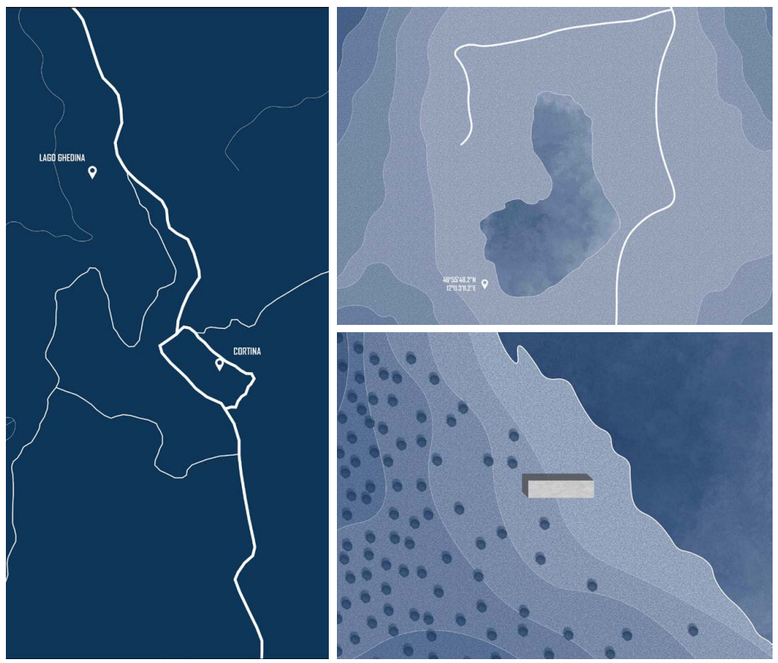







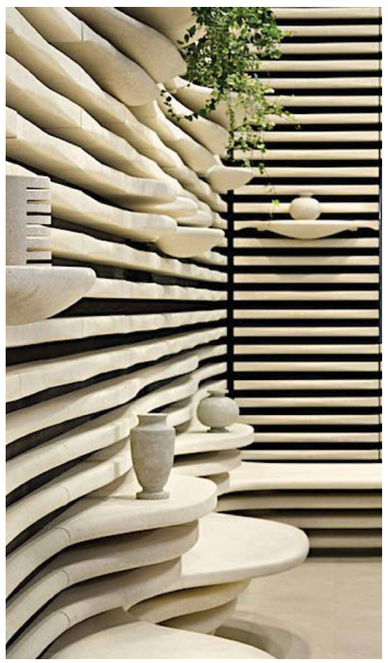



Pianta e sezioni

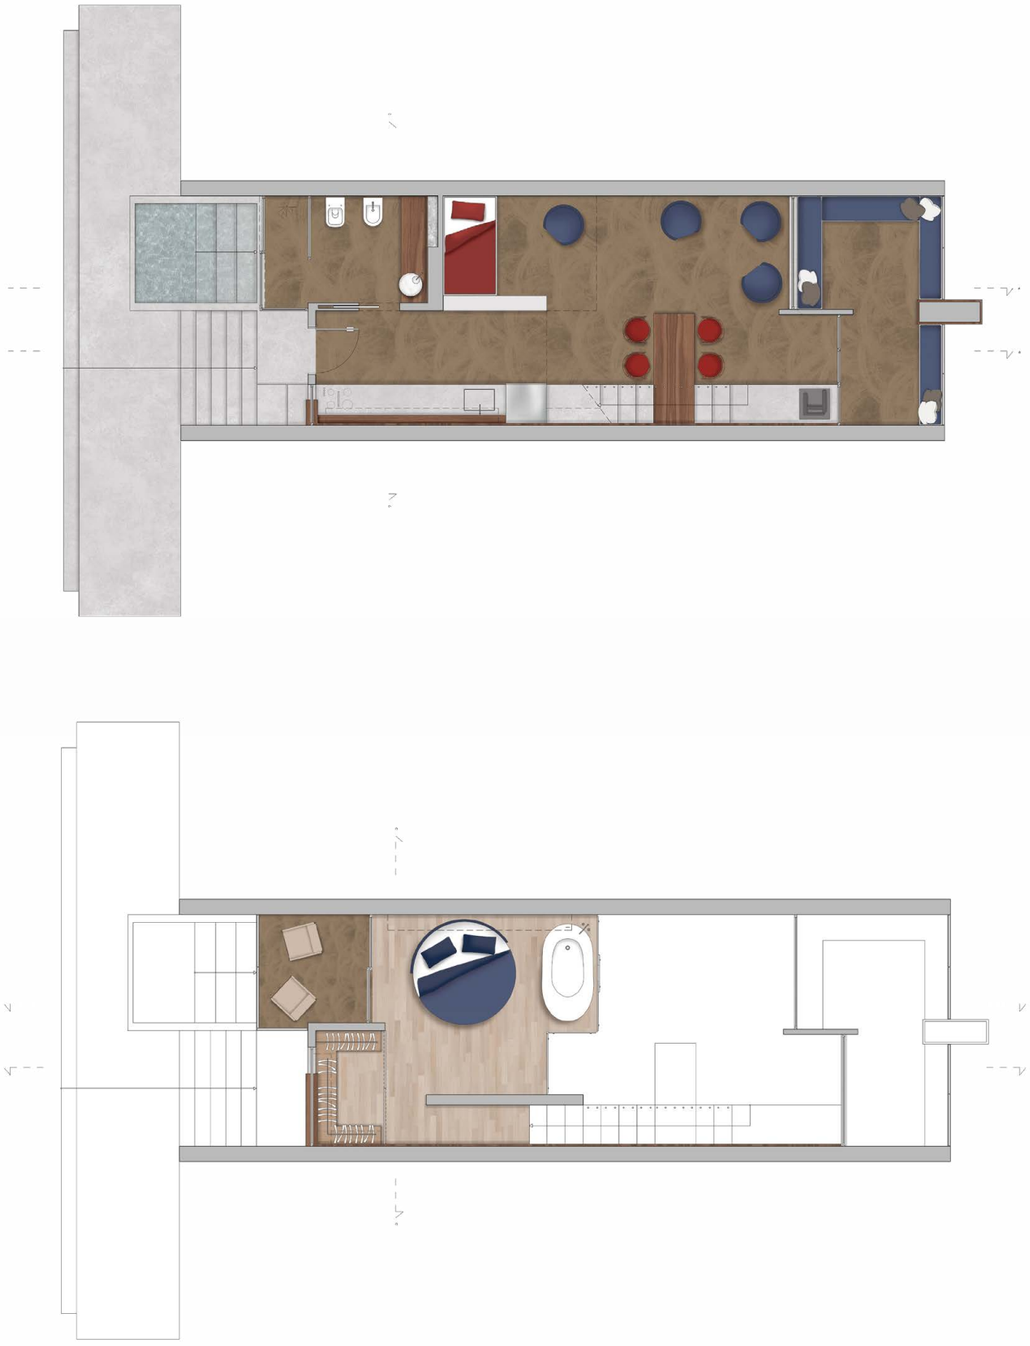

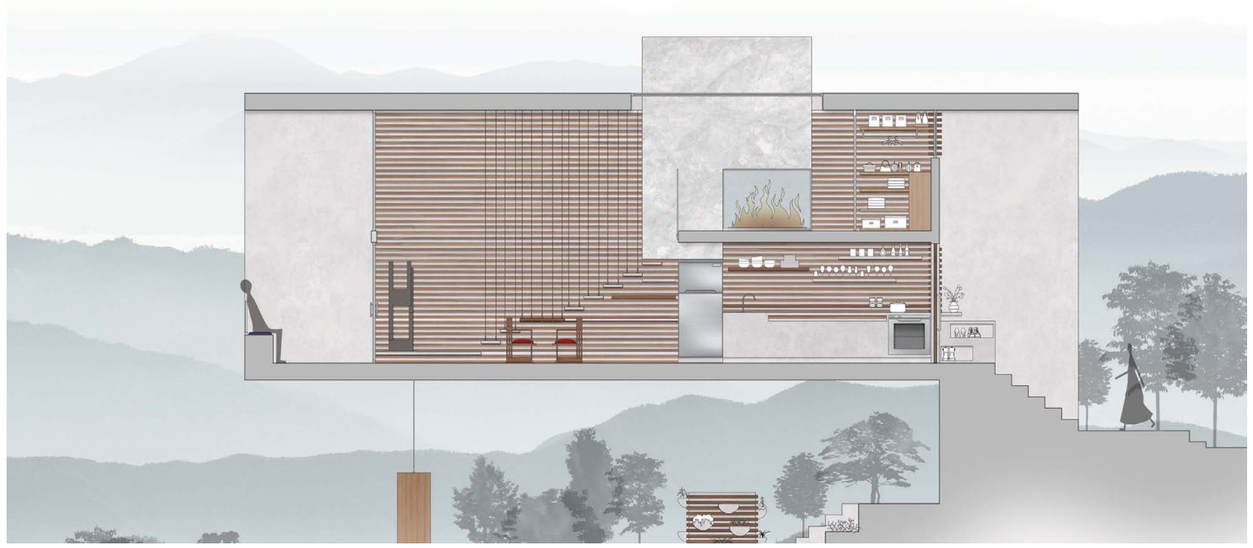



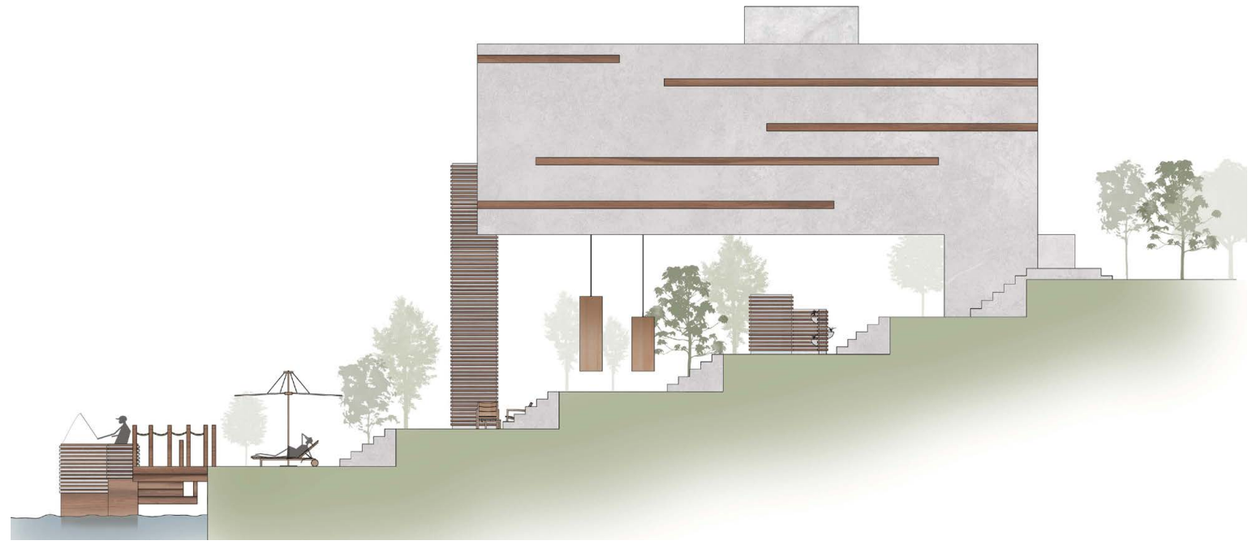


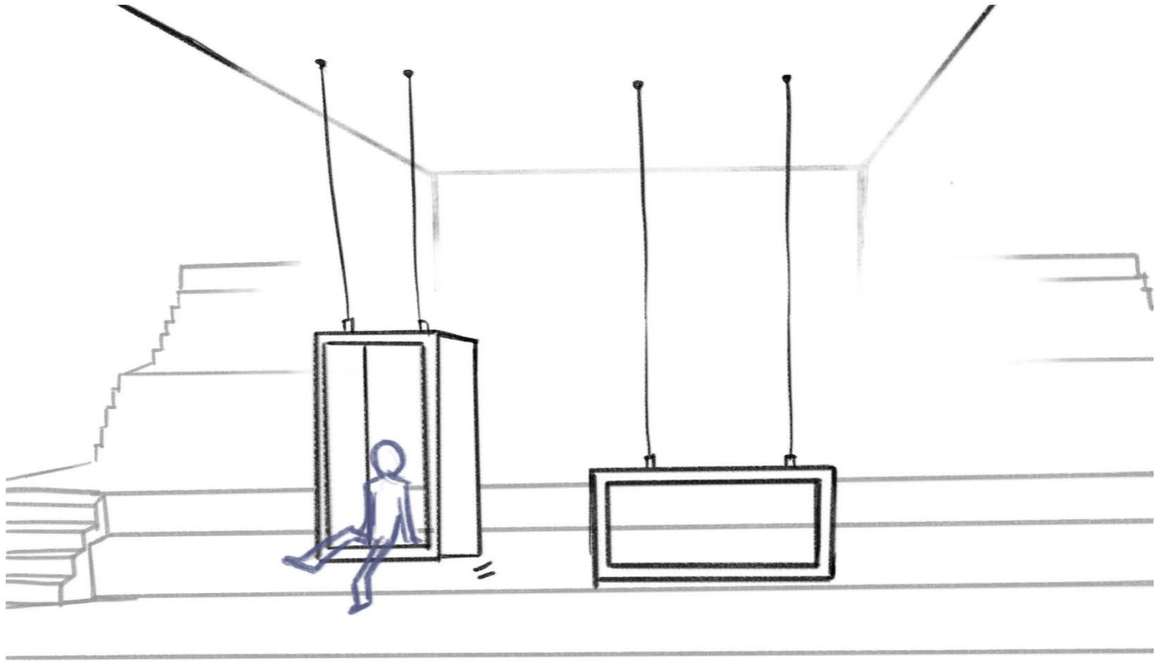







Terrazzamento esterno

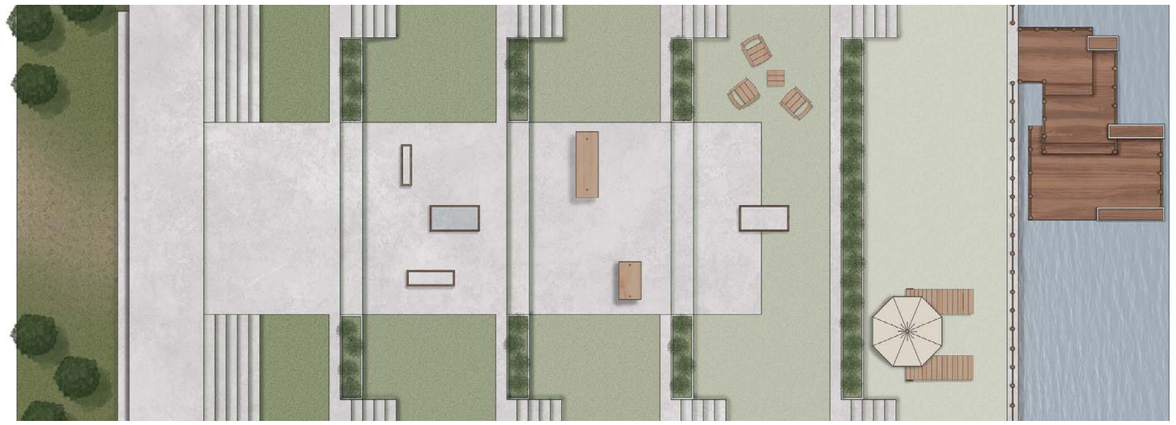

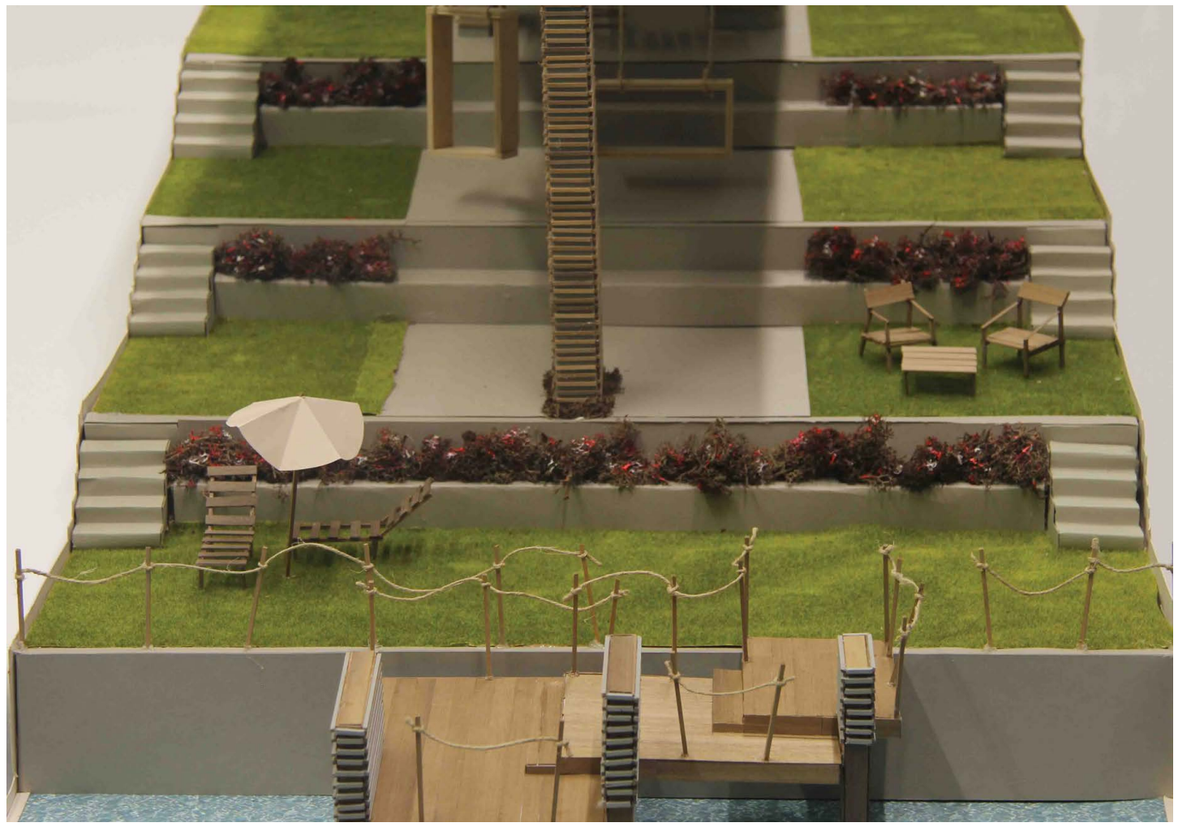






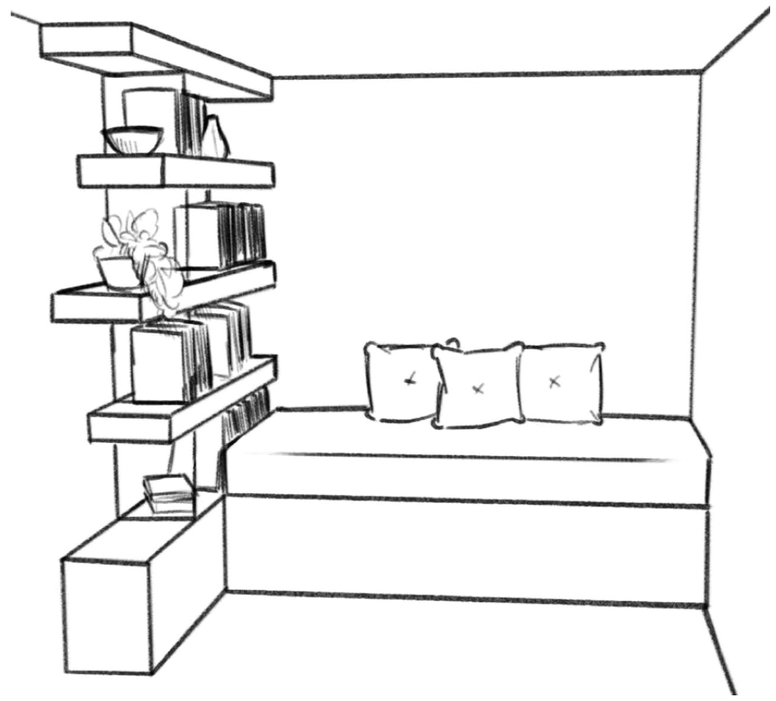




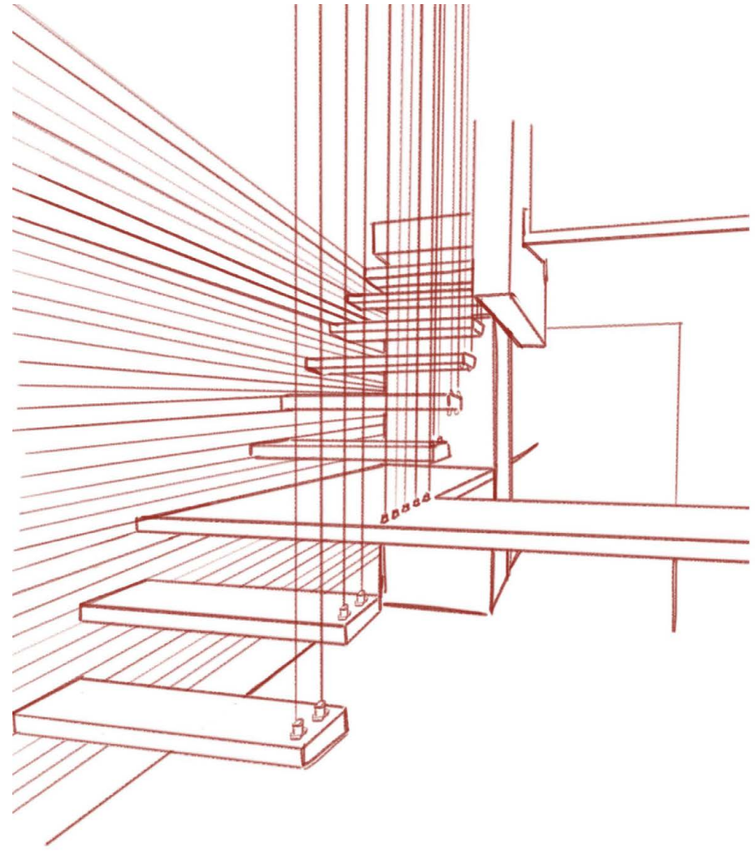


Modello



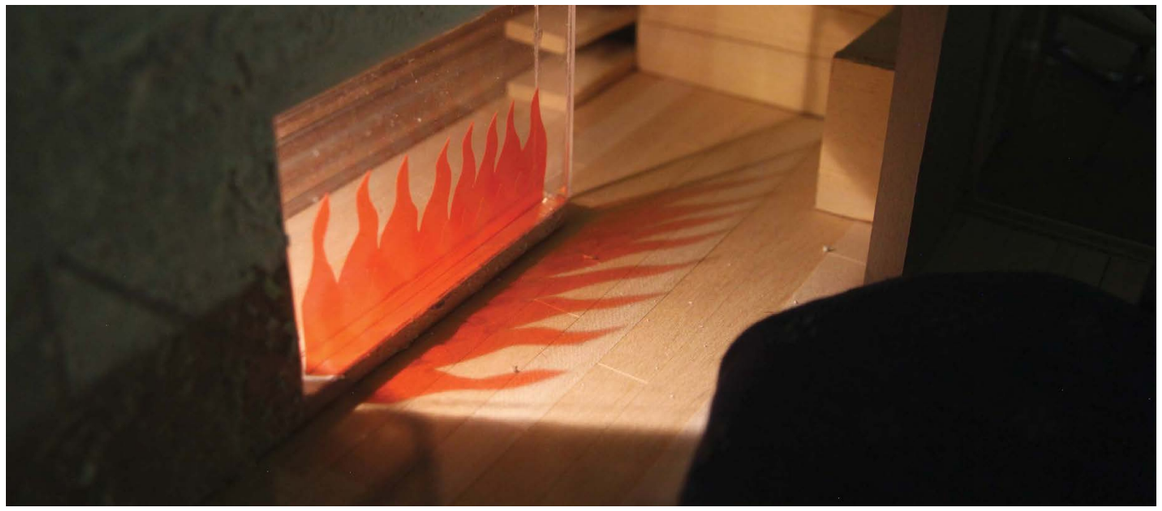





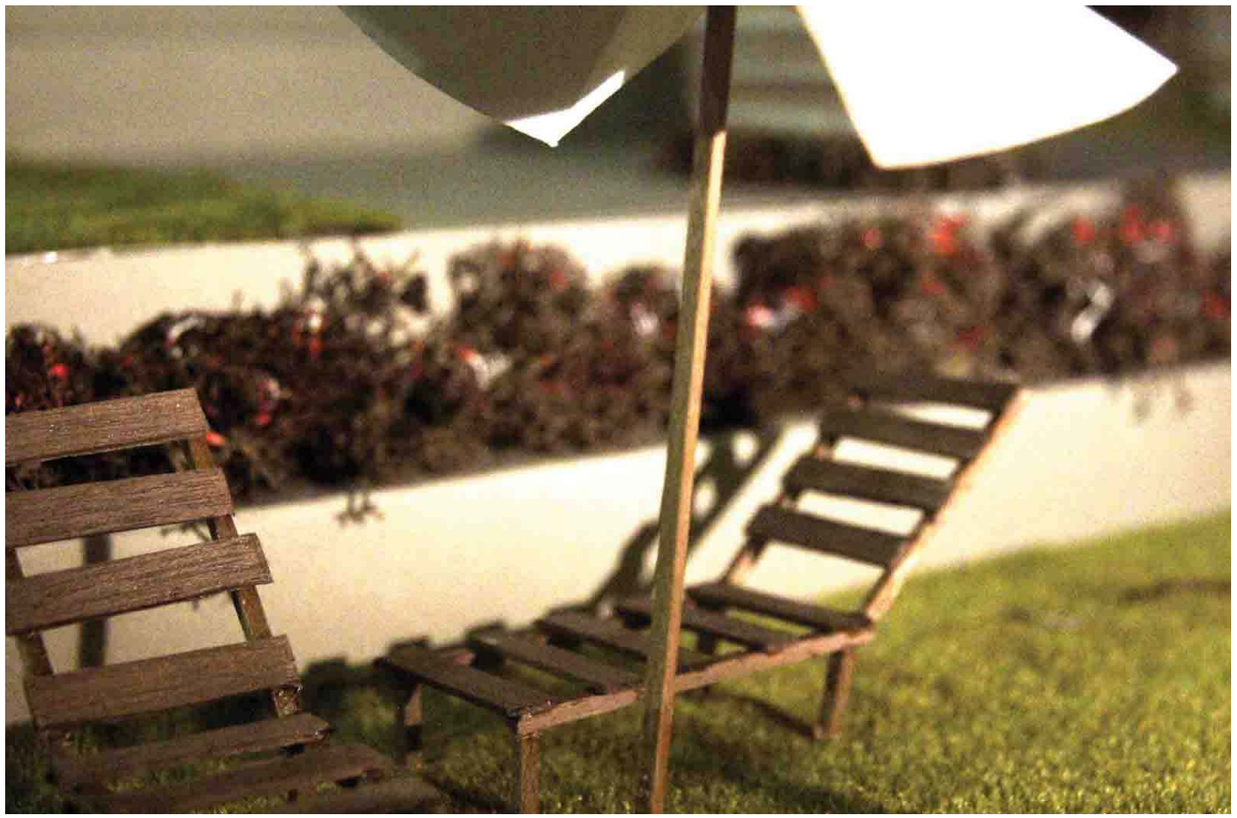

04

Uno + Uno

Corso
Politecnico di Milano, secondo anno, Laboratorio di metaprogetto
Docenti
L.Brenna, A. Colombo, A.Rebaglio
Progettisti
Jacopo Dellanoce, Elisa Sofia Jansson, Edoardo perina

Sito di progetto

Cascina Linterno.


Un luogo che raccoglie secoli di storia. Situata nel Comune di Milano in Via Fratelli Zoia, presso il Parco delle Cave, accoglie inizialmente una comunità di templari. Già nel 1154 viene citata in una pergamena con il nome di “Infernum”; nel XII secolo rappresentava un luogo di passaggio poiché crocevia di strade di pellegrinaggio.

Concept


UNO + UNO si basa sull’unità singola e sull’unione di quest’ultima ad altre unità uguali. Un quadrato è una figura geometrica che si forma attraverso quattro linee rette uguali, che si incontrano ad angoli retti, creando una forma chiusa. Il quadrato è quindi un sistema di linee rette che si intersecano per definire uno spazio ordinato e simmetrico, che esprime armonia ed equilibrio.La perfetta unione tra questi elementi e concetti è rappresentata dall’utilizzo di una griglia regolare, di modulo 60 x 60 centimetri. La griglia è una rappresentazione visiva della logica, poiché si basa su principi fondamentali di ordine e coerenza, gli stessi che governano il pensiero logico e che sono strettamente legati a ragione e conoscenza.

Tema


Il cohousing nasce ufficialmente in Danimarca negli anni Sessanta. Il pioniere di questo movimento è l’architetto danese Jan Gudmand-Høyer (1936 - 2017), che nel 1964 propone un nuovo tipo di abitazione in cui le famiglie possano condividere spazi come cucine, sale comuni e giardini, mantenendo però la propria privacy nelle abitazioni private.Con cohousing si intende quindi la condivisione di spazi e servizi da parte di chi vive in unità abitative indipendenti, ma situate in uno stesso complesso. In sintesi si tratta di abitazioni private, con servizi in comune e spazi condivisi che si basa sull’equilibrio tra il rispetto della privacy e la possibilità di svolgere una vita sociale e comunitaria.

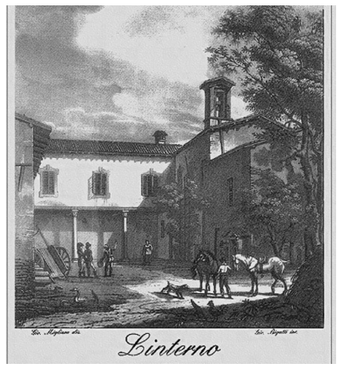




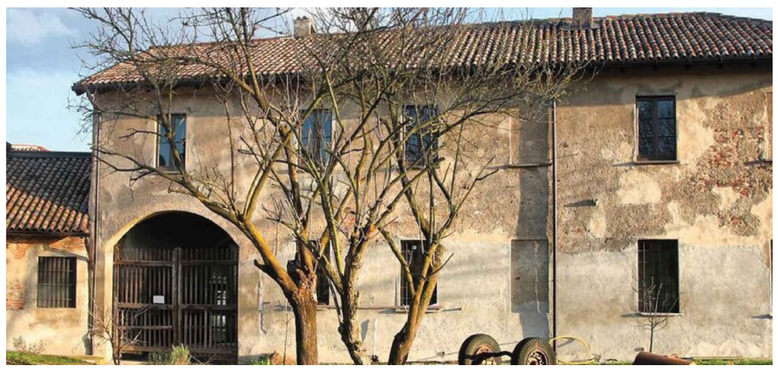


Ripetizione

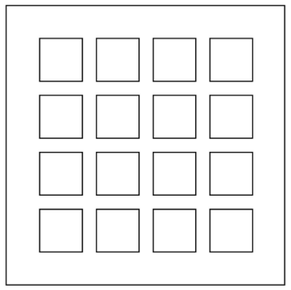


Forma chiusa

 

Enfasi

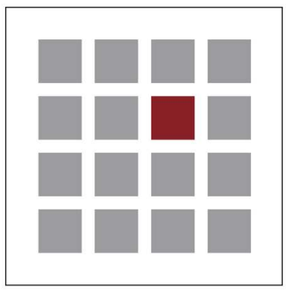


Ortogonalità

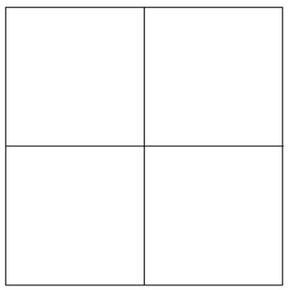







Pianta e sezione

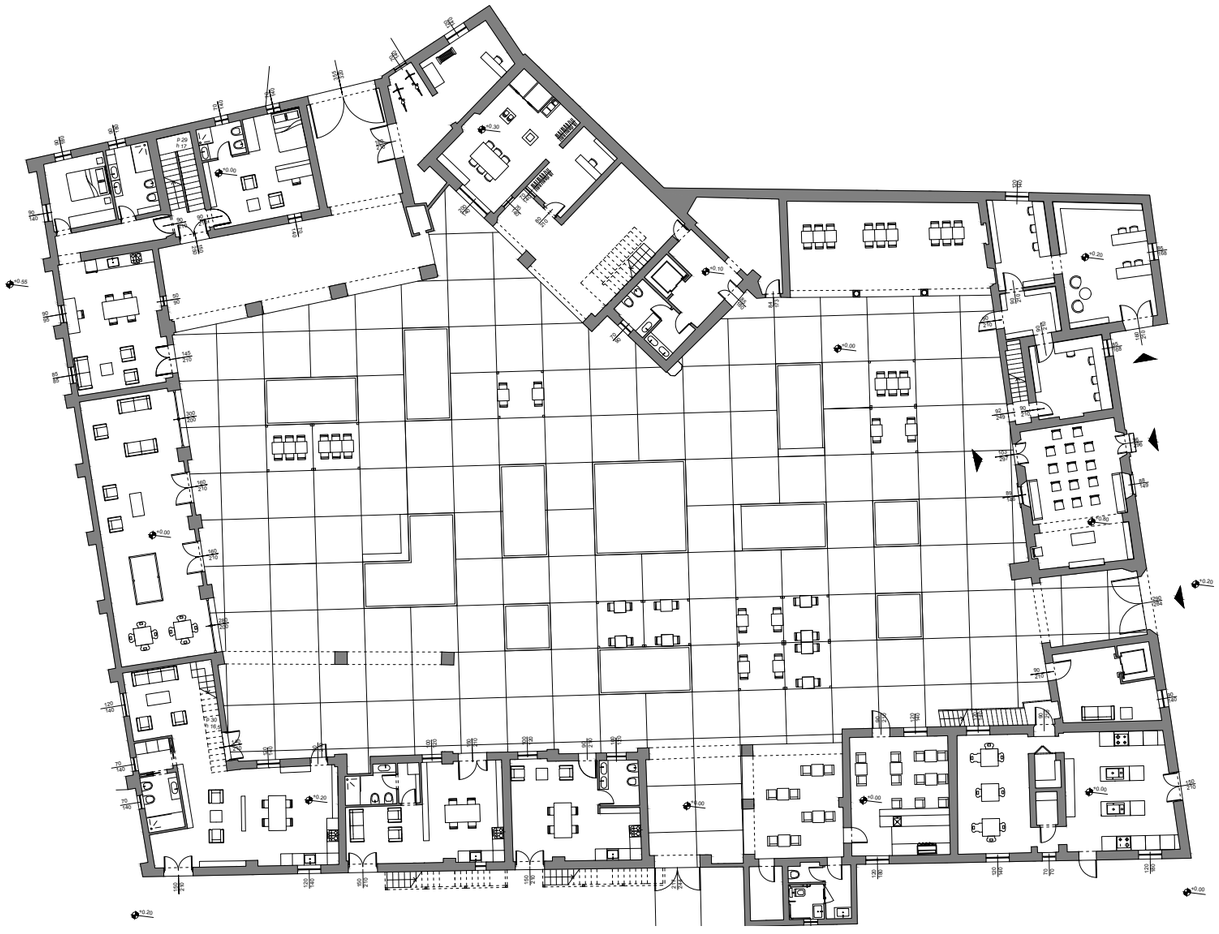

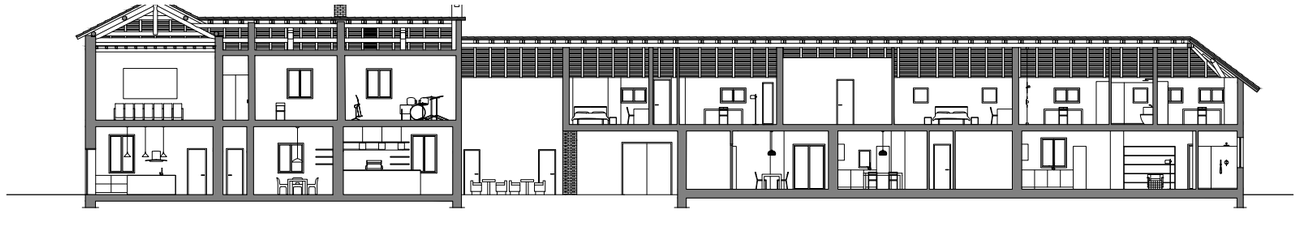

Caso studio


Superstudio è stato un gruppo di architetti italiani fondato a Firenze nel 1966 da Adolfo Natalini e Cristiano Toraldo di Francia. Inserito nel movimento dell'architettura radicale, il collettivo ha rivoluzionato il panorama architettonico e culturale degli anni '60 e '70. Il loro approccio era profondamente critico nei confronti del modernismo funzionalista e della crescente mercificazione dell'architettura, proponendo invece un'idea visionaria che utilizzava l'architettura come mezzo per esplorare tematiche filosofiche, sociali ed estetiche. Simbolo di questo pensiero è "Monumento Continuo", una struttura immaginaria che si estende all'infinito sul pianeta.

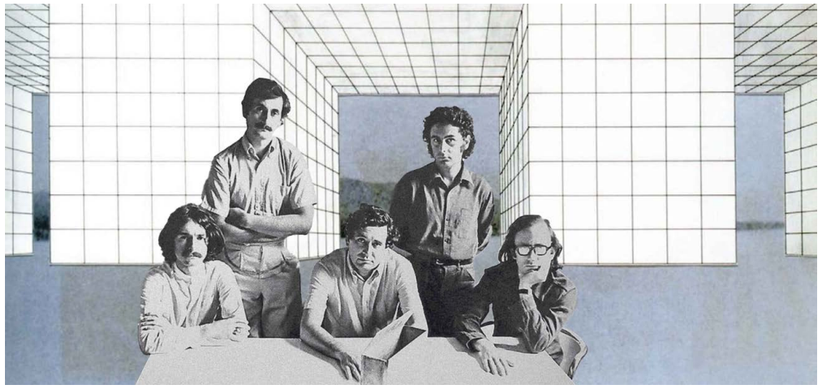




Corte interna


La corte interna di Cascina Linterno rappresenta un luogo centrale di socialità, condivisione e relax, dove gli abitanti possono incontrarsi, organizzare eventi, scambiare idee e stare all'aria aperta. All'interno della Cascina sono presenti numerose aree aperte ad un pubblico esterno, come una biblioteca ed un bar, che si affacciano sulla corte centrale e che rendono il complesso simile ad un piccolo villaggio. Da un punto di vista progettuale, la corte è ispirata alla tipica piaza italiana ed è ricoperta da una pavimentazione costituita da sanpietrini, in una griglia regolare ortogonale di modulo 240 x 240 centimetri. Il verde è racchiuso all'interno di grandi vasi, anch'essi ortogonali e risultanti da un'estrusione della griglia principale, sui quali sono disposte delle sedute.Popolano l'ambiente una serie di gazebo attrezzati con tavoli e sedie, leggeri e resistenti, pensati per una veloce partita a carte, una tranquilla conversazione o del semplice relax.Nel centro geometrico della corte è infine presente una grande vasca d'acqua, a ricordare le fontane spesso presenti nelle principali piazze italiane.

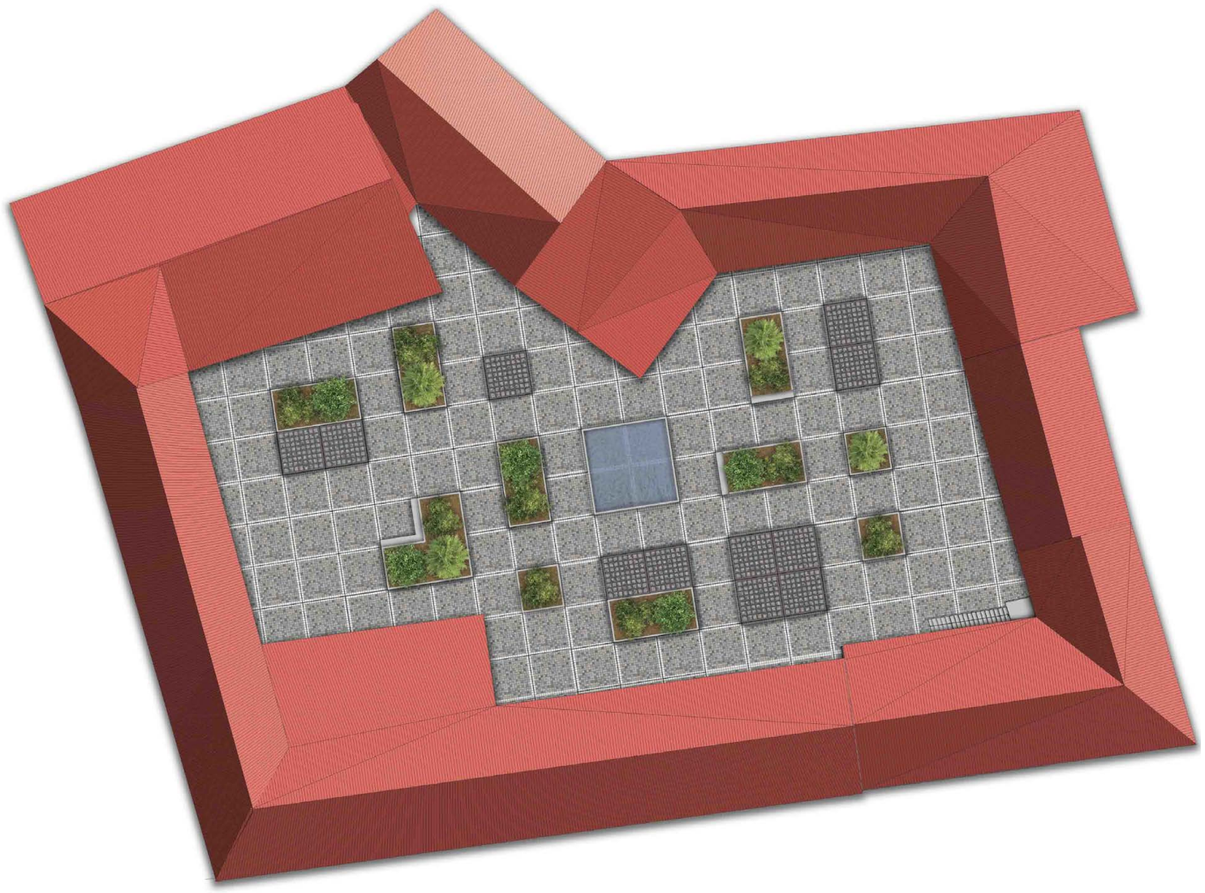



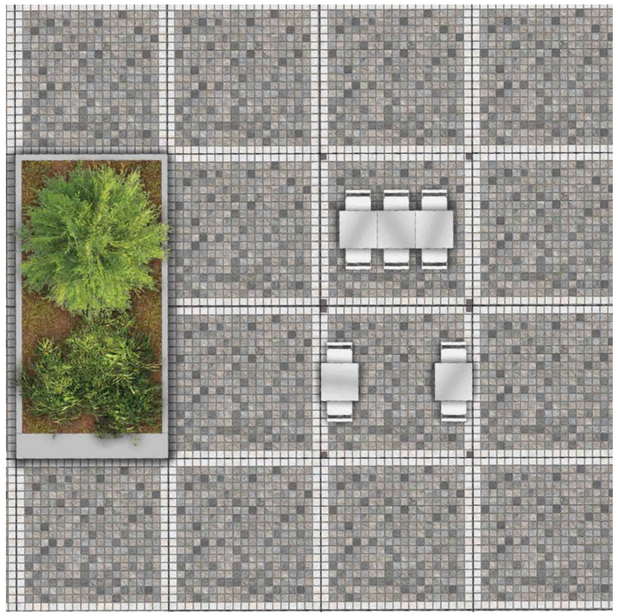




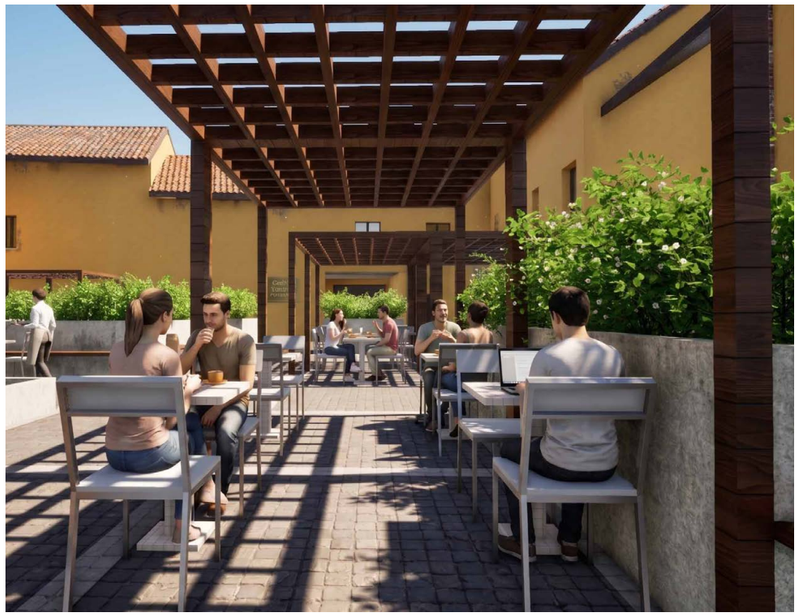



Bar


Il bar di Cascina Linterno rappresenta l'estremizzazione dell'idea progettuale di griglia e quadrato.Ispirato dalla mostra "Between the lines" di Luigi Ghirri a Casa Mutina Milano, il bar presenta arredi progettati appositamente per l'ambiente, dai colori accesi e completamente ricoperti da piastrelle quadrate.Ogni superficie, dal bancone al pavimento, è rivestito da piastrelle quadrate che rispettano ancora una volta le proporzioni della griglia principale.Il bar di Cascina Linterno vuole rappresentare un esempio senza precedenti, ed essere visto come una curiosità e un'esperienza, in grado di avvicinare le persone a questo centro.


Luigi Ghirri | Between the lines

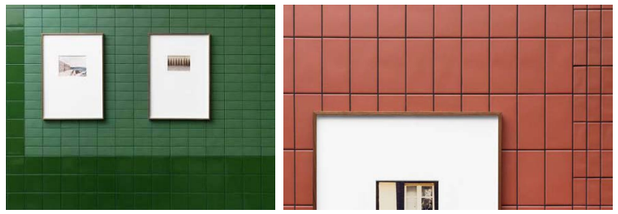

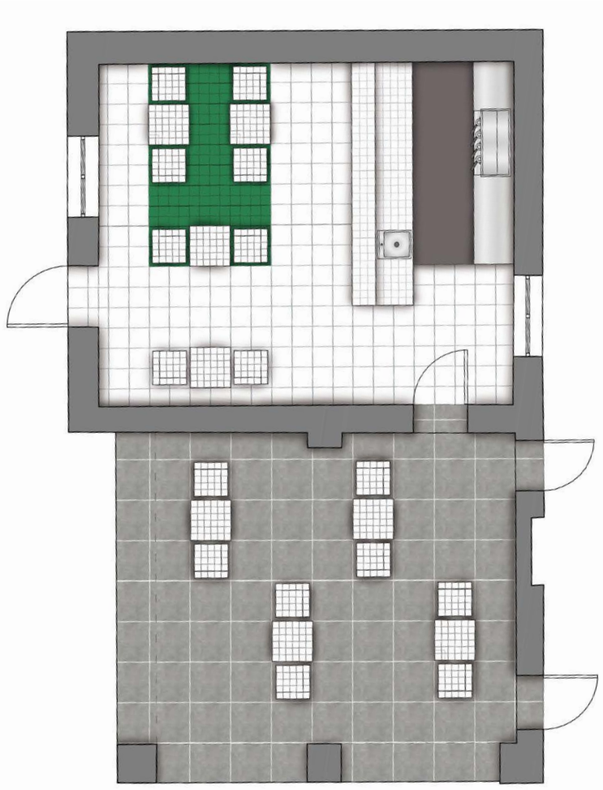


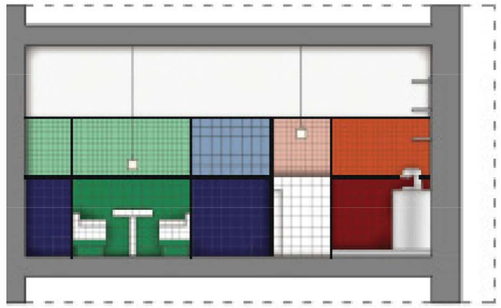


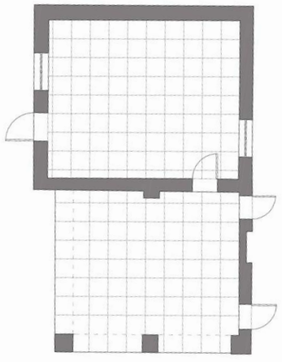

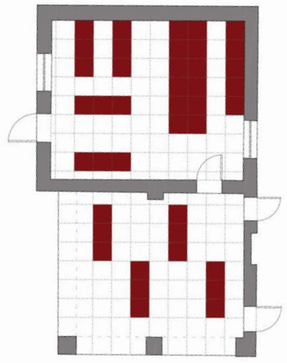





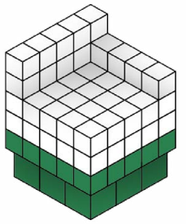


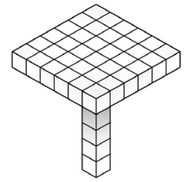

griglia di modulo 60x60 centimetri. Qui le aree colorate segnano la presenza di tavoli, sedute e del bancone bar. In questa zona i quadrati della griglia diventano una vera e propria estrusione.

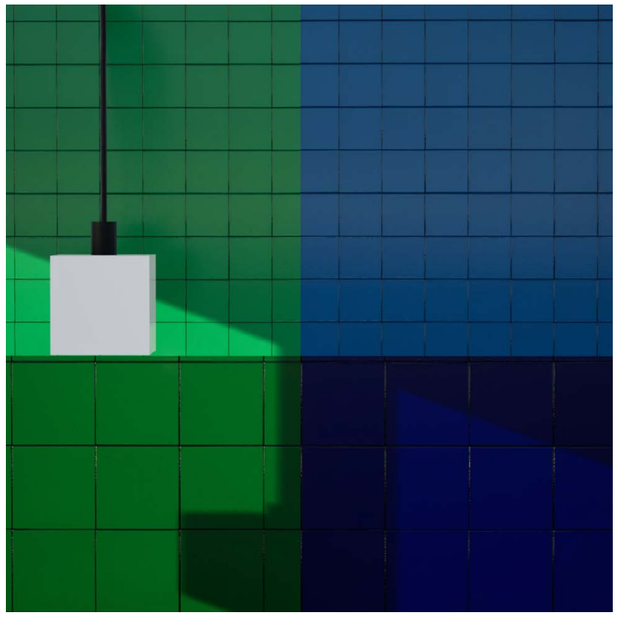


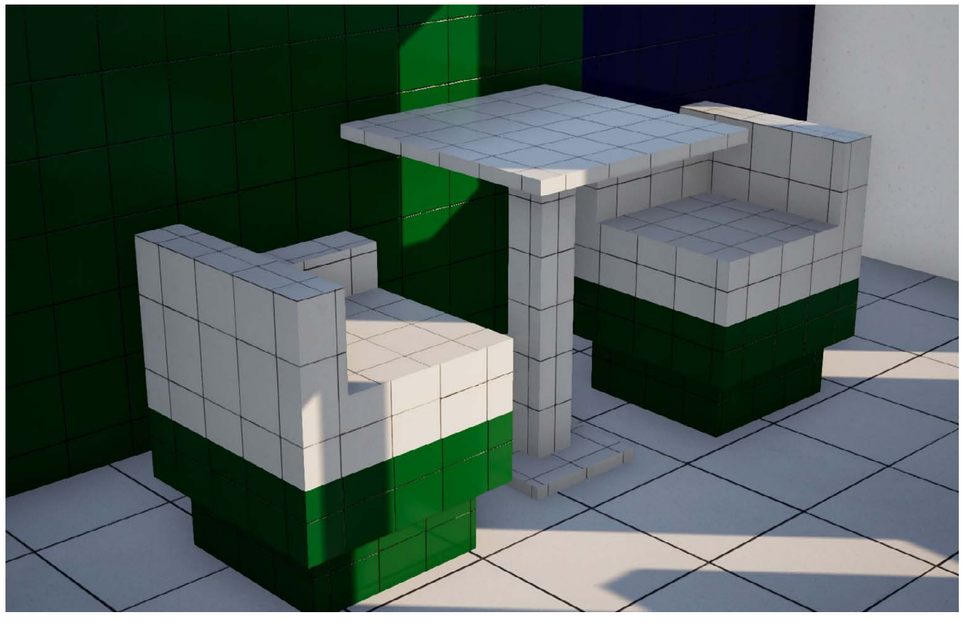

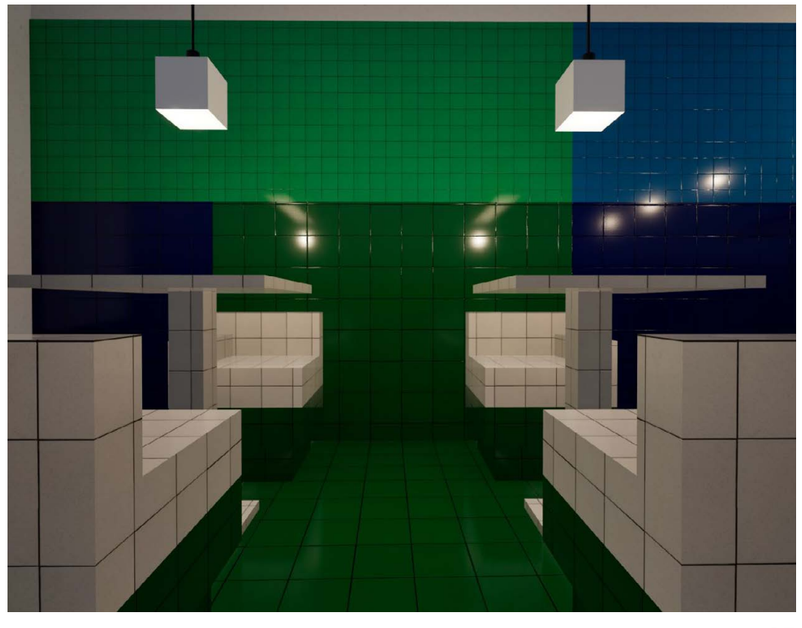

Alloggio

All’interno della cascina sono presenti varie tipologie di alloggio: a partire da una dimensione più piccola, adatta a ospiti che vi soggiornano per una quantità di tempo inferiore, fino ad arrivare a duplex ad ampia metratura, in grado di ospitare fino a tre persone. Tutti però condividono le stesse caratteristiche progettuali: si basano su una griglia, di modulo 60x60 centimetri, che divide gli spazi in zone funzionali e che aiuta a creare un ordine geometrico e una pulizia visiva.Gli arredi si avvicinano all’estetica razionalista: forme geometriche ed essenziali, senza dettagli superflui, realizzate in materiali moderni. Ricordano linea retta e al quadrato, punti saldi del progetto. Inoltre, superfici e arredi stessi sono ricoperti e formati da piastrelle di forma quadrata, che rispettano le dimensioni e la direzione della griglia principale.I colori vogliono richiamare il razionalismo internazionale e italiano: sono tenui e leggeri, poco brillanti, con dettagli più vivaci rappresentati dalle piastrelle

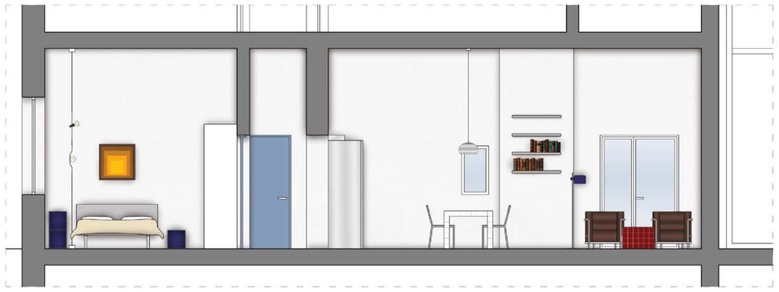








griglia regolare ortogonale formata da quadrati di modulo 60x60 centimetri. Lo spazio viene modellato dalla griglia e vengono così a formarsi diverse zone funzionali. I quadrati colorati indicano il collocamento di elementi d’arredo e materiali che seguono la griglia.

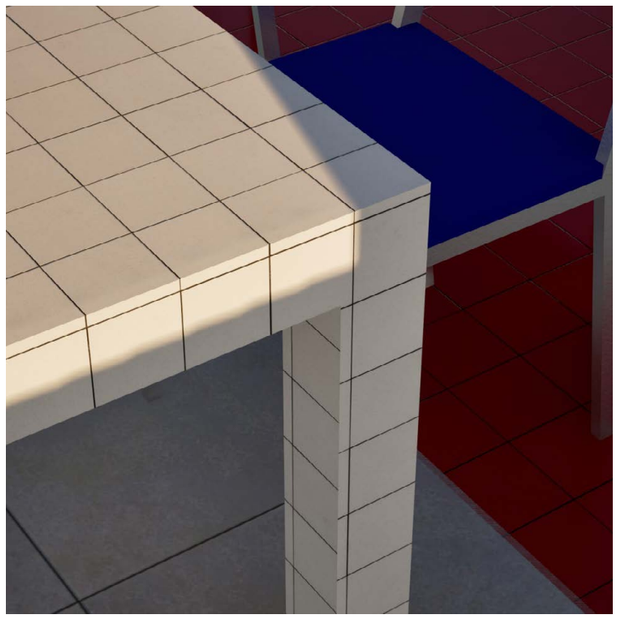






Mostra





Modello



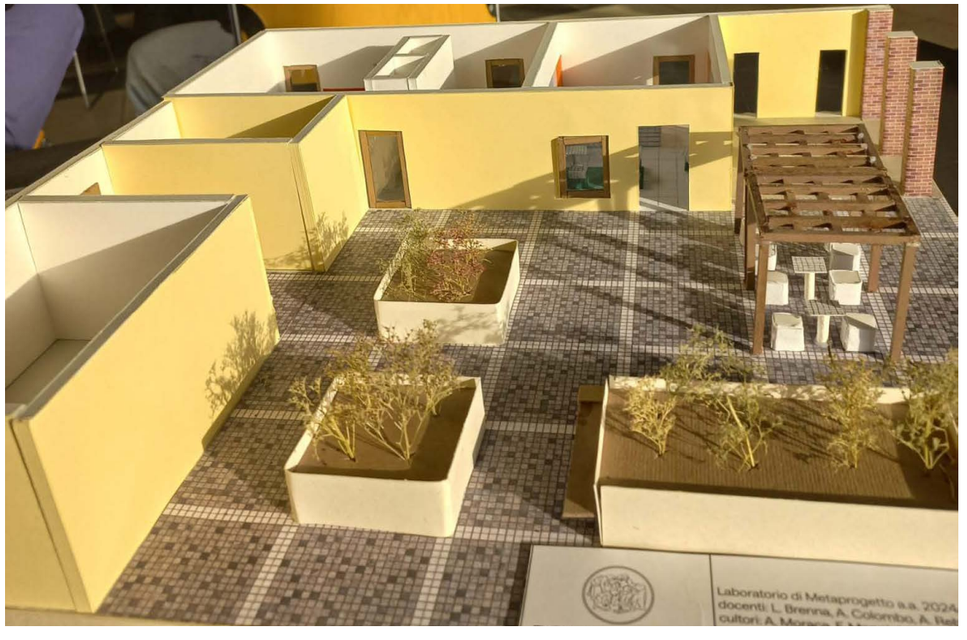



05
Workshop


Corso
Politecnico di Milano, terzo anno, Workshop progettare l'avanzo, Villaggio Alpino TCI di Valganna
Docenti
Luciano Crespi, Lucia Ratti, Marco Splendore
Progettisti
Jacopo Dellanoce, Leonardo Goldstein Bolocan, Giada Piccinno, Giorgia Ricci


La riflessione è scaturita da una scritta presente sul muro dell'Avanzo, che ha catturato la nostra attenzione durante il sopraluogo. Comunque adesso ho un po' paura è un verso della canzone Il Nastro Rosa di Lucio Battisti, che ha consentivo di svilluppare il concept alla base della nostra nuova versione di Colonia per bambini. Abbiamo analizzato una serie di avventure che i bambini desiderano compiere durante l'esperienza della colonia: dalle più fantasiose, sognanti a quelle più pre adolescenziale e relazionali.

Ognuna di queste avventure é connaturata da una paura associata che sembra frenare il bambino dal viverla in maniera completamente spontanea. Per questo il nostro progetto si propone di creare spazi e soluzioni sincere in grado di favorire le avventure minimizzandone le paure. Spazi che invitano all'interazione come strategia per affrontare e gestire la paura che alle volte può paralizzare…







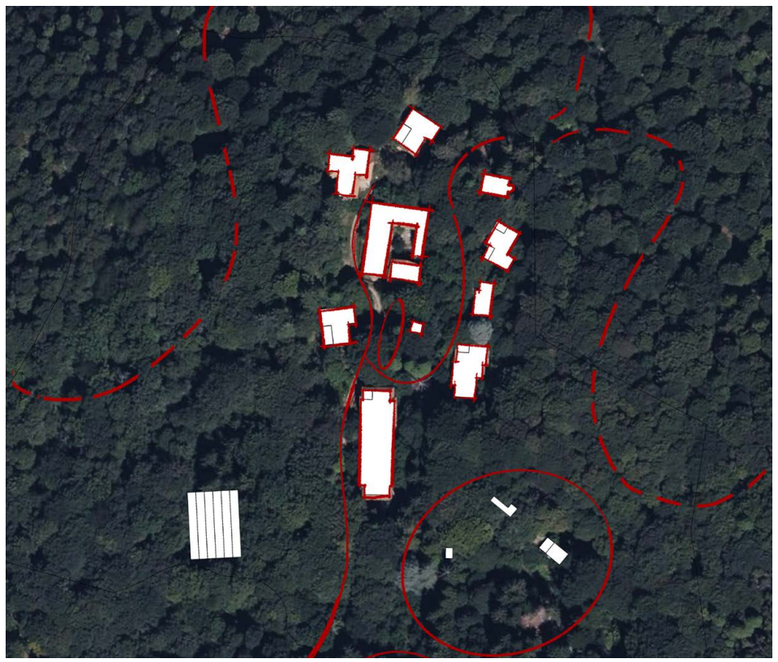

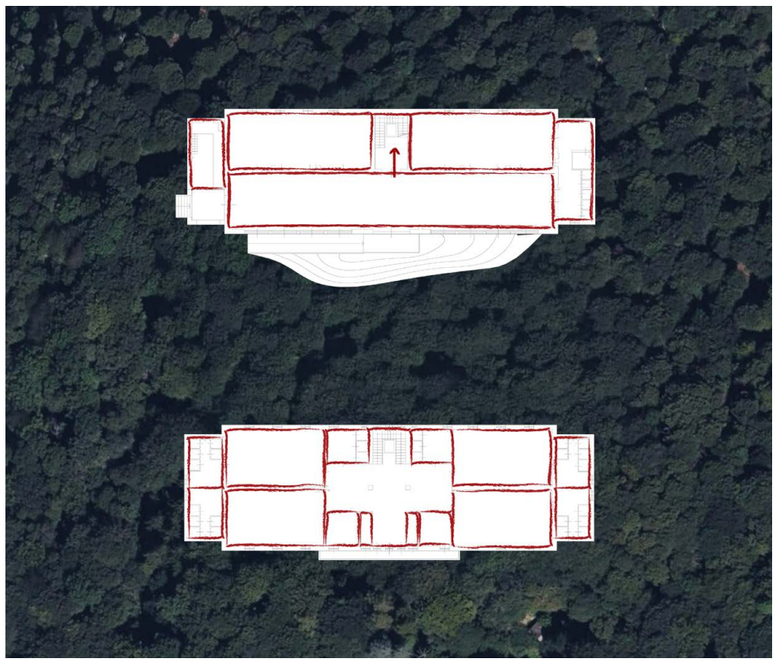

Pianta del progetto

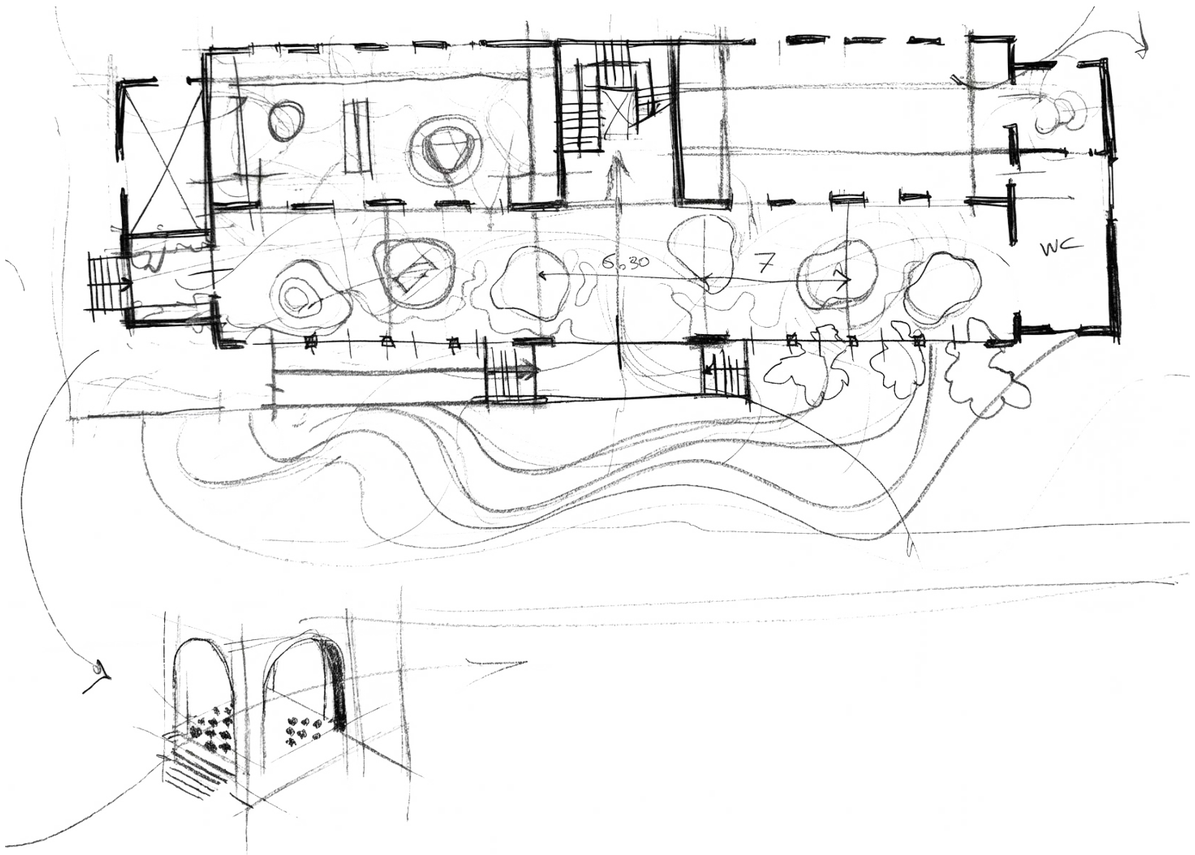

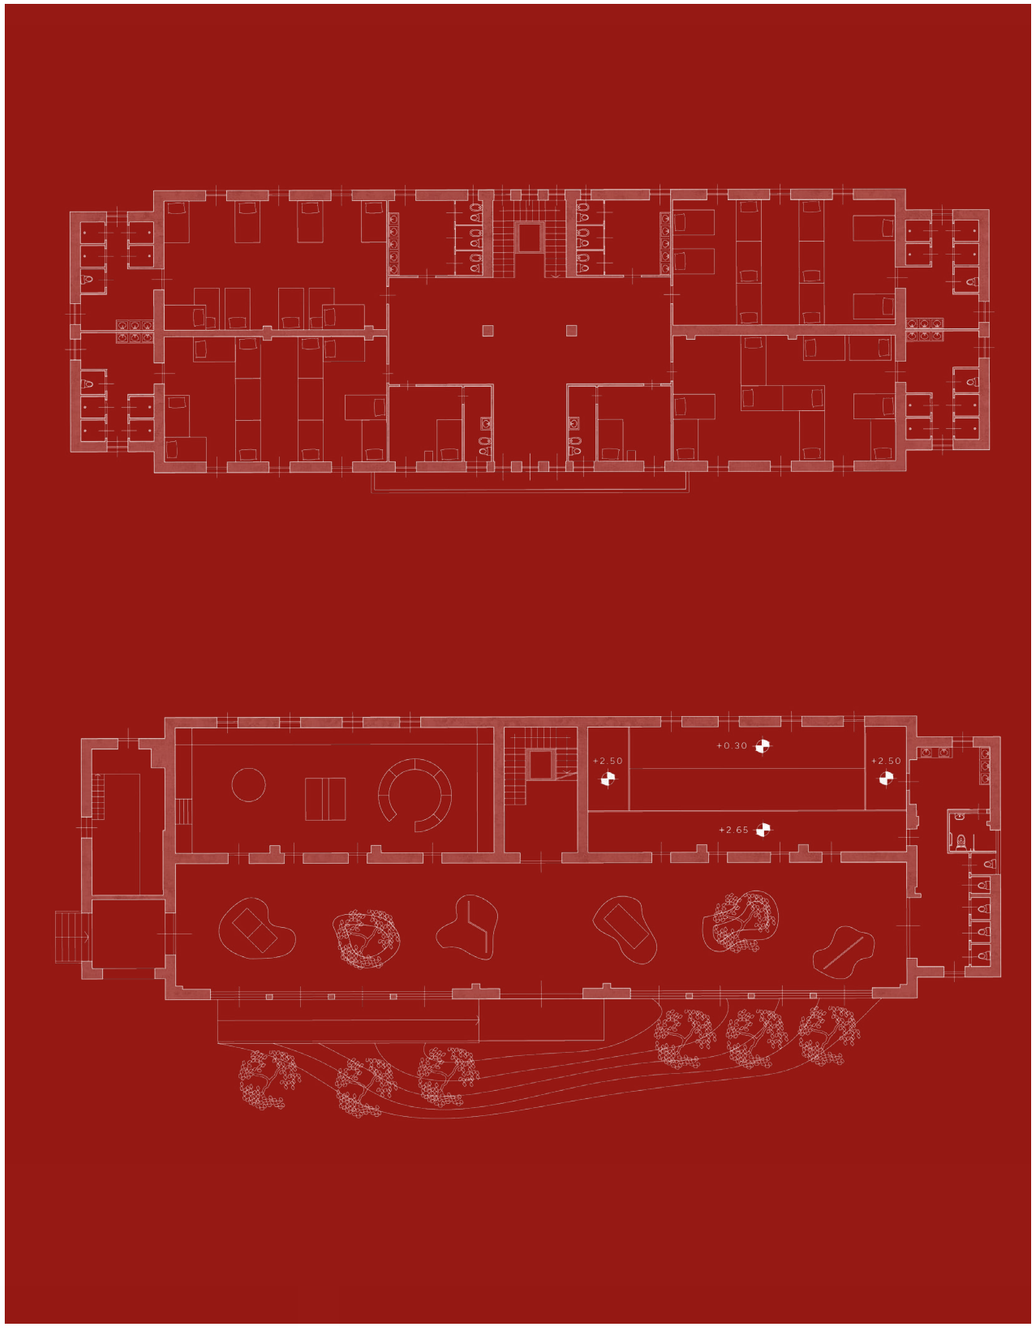





AVVENTURA	PAURA	SPAZIO CONCRETO
giocare senza telefono	annoiarsi	spazio gioco
mostrare il mio talento	paure di esporsi	spazio espositivo
guardare oltre	paura dell'ignoto	osservatorio
essere protagonista	paura di parlare in pubblico	teatro - cinema
scrivere la propria storia	paura del giudizio	laboratorio di scrittura

AVVENTURA	PAURA	SPAZIO CONCRETO
giocare tutto il giorno	non potrei fare per colpa della pioggia	spazio gioco
costruire qualcosa di magico	non trovare la persone magica	laboratorio creativo-manuale
mangiare tutto quello che voglio	dover mangiare le verdure	laboratorio di cucina
proteggere il mondo delle fate	la natura è un pericolo!	laboratorio di didattica ambientale
dormire lontano da casa	dormire contano da casa	dormitorio

Spazio interno-esterno

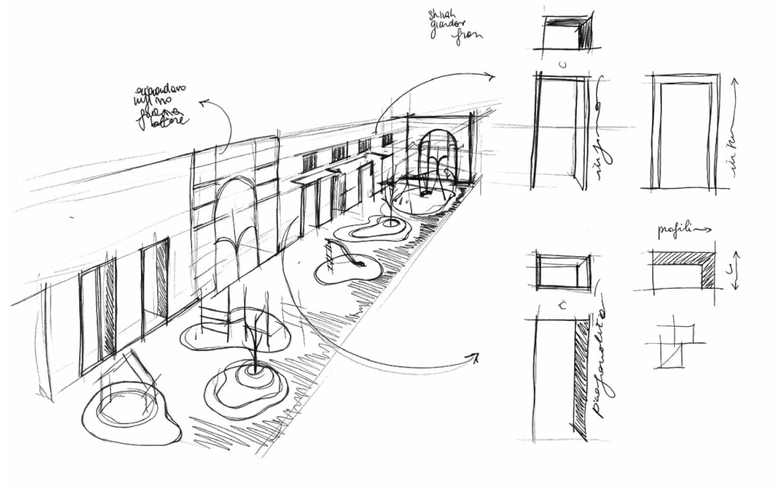

Spazio gioco

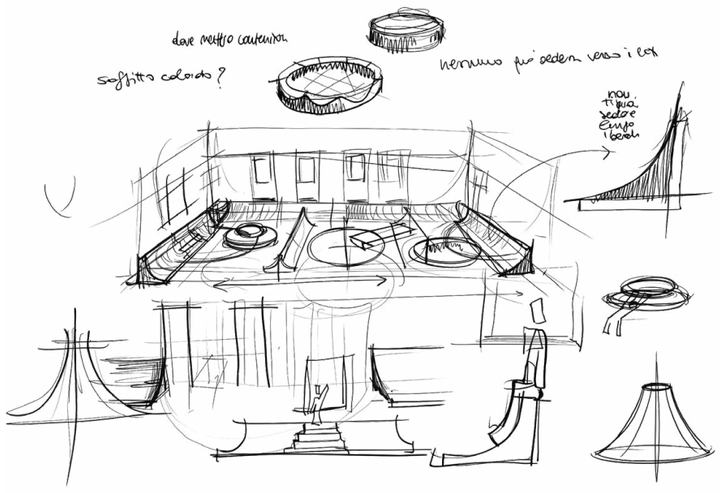

Chiesetta











Dormitorio bambini

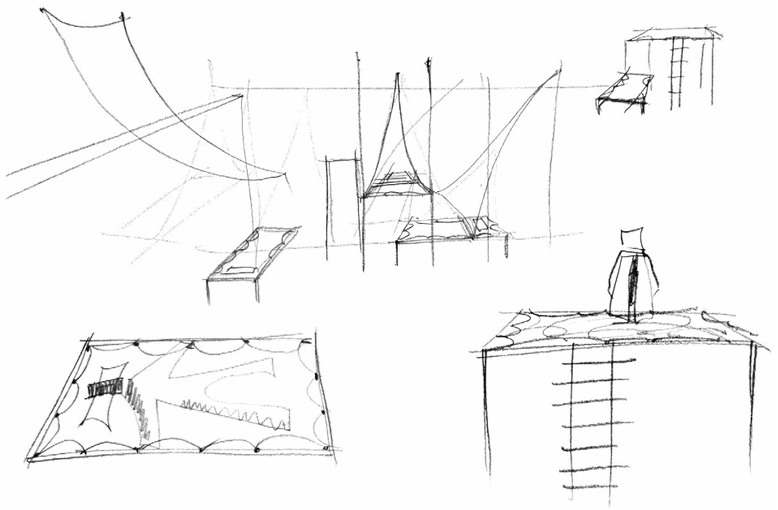

Spazio gioco

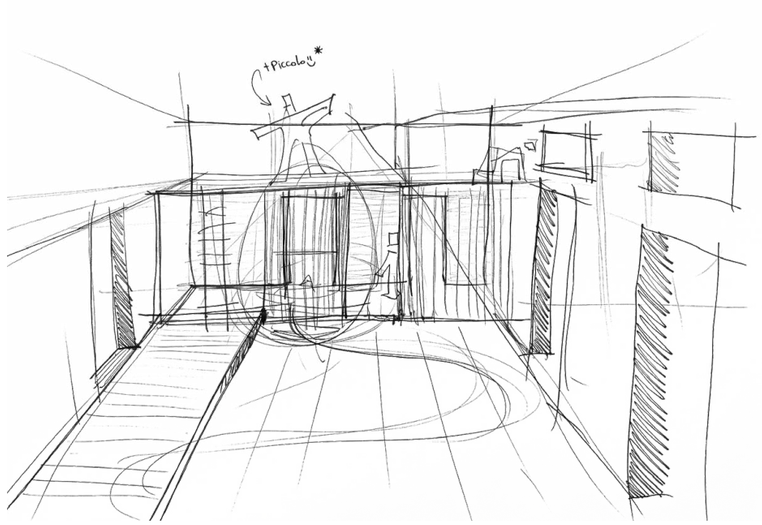

Capannina

